Nº	RAIO (m)	LC	ÂNGULO CENTRAL/ RUMO	D/DC (m)	TG (m)	PONTOs NOTÁVEIS	km	NORTE	LESTE
			N05° 58' 45,32"E		1674,815	ST	426+537,836	9528845,476	533159,646
		50				TS	428+212,652	9530511,180	533334,109
C-27	1500		N5° 01' 41"W	526,344		SC PI CS	428+262,652 428+528,558 428+788,996	9530560,935 9530826,240 9531082,568	533339,041 533367,108 533293,146
		50				CS	428+788,996	9531082,568	533293,146
			N16° 02' 07,72"W		194,442	ST	428+838,996	9531130,698	533279,602

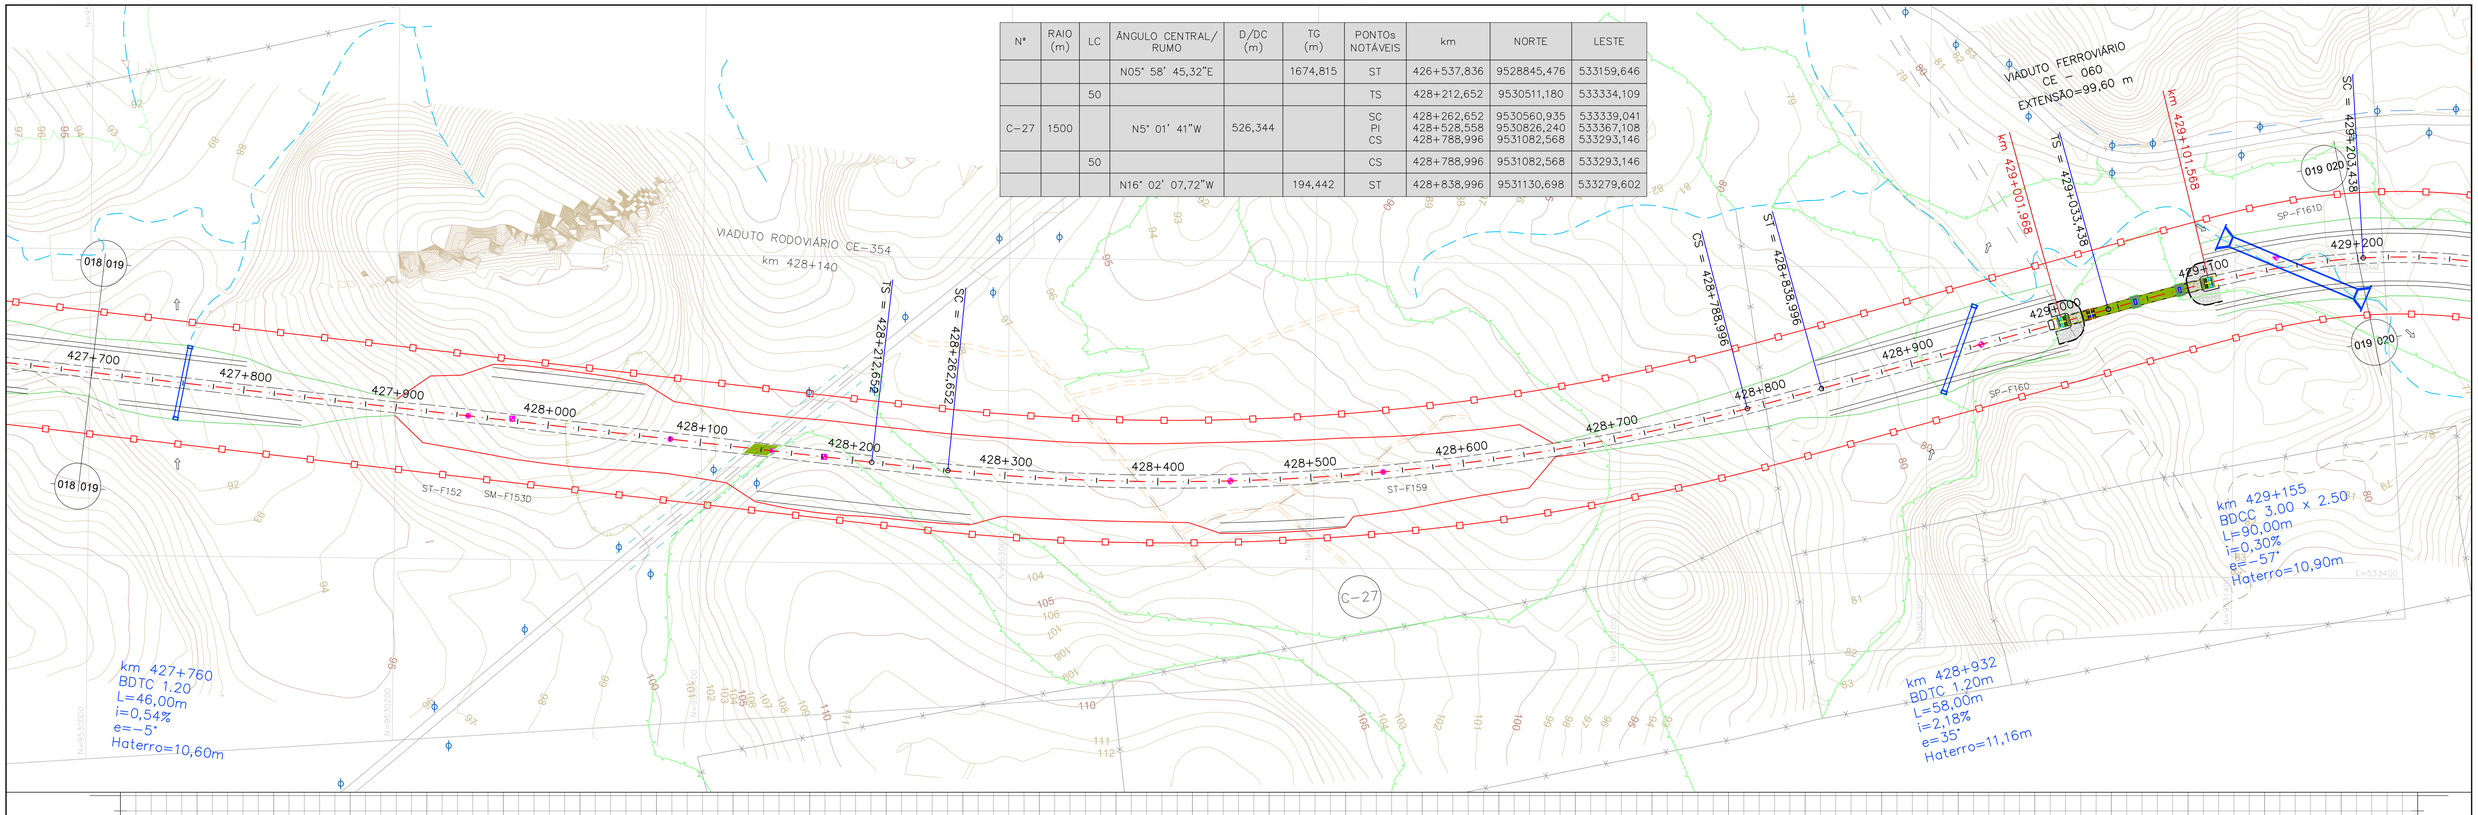

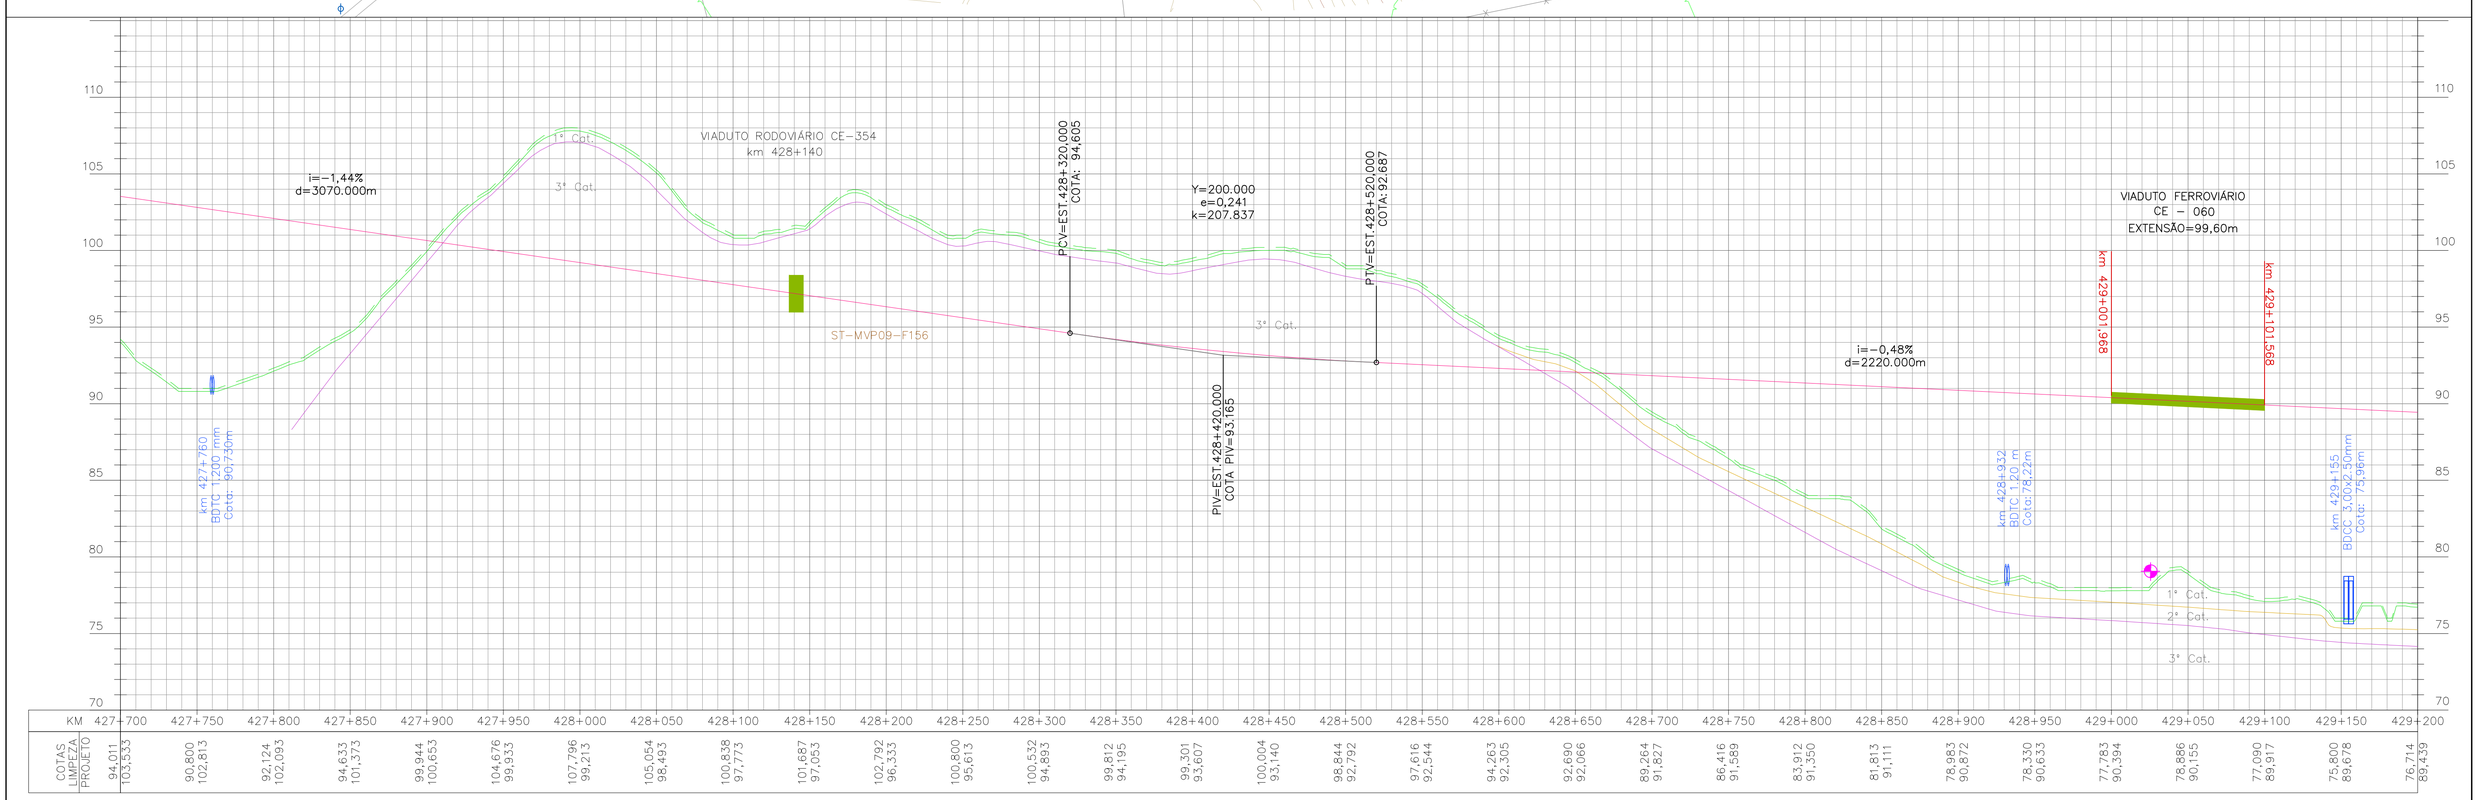

Nº	DESCRIÇÃO	DATA	EMITENTE	VERIFICAÇÃO	APROVAÇÃO
01	REVISÃO DE FAIXA DE DOMÍNIO	02/04/2026	RSC	LAPB	UAS
00	EMISSÃO INICIAL	18/10/2024	INDS	LAPB	UAS

REVISÕES

CÓDIGO	OBJETO

DOCUMENTOS DE REFERÊNCIA

TLSA TRANSNORDESTINA LOGÍSTICA S.A.

		SIGLA	VERIFICAÇÃO	APROVAÇÃO
Desenho:	IANYE NASCIMENTO DA SILVA			
Projeto:	IANYE NASCIMENTO DA SILVA			
Verificação:	LARISSA ARAÚJO DE P. BARBOSA			
Resp. Téc.:	UINNE ANTUNES SILVEIRA			

ESTA FOLHA É PROPRIEDADE DA TLSA TRANSNORDESTINA LOGÍSTICA S/A E SEU CONTEÚDO NÃO PODE SER COPIADO OU REVELADO A TERCEIROS. A LIBERAÇÃO OU A APROVAÇÃO DESTE DOCUMENTO NÃO EXIME A DETALHISTA DE SUA RESPONSABILIDADE SOBRE O MESMO.

TRANSNORDESTINA Logística S.A.

LINHA:	FERROVIA TRANSNORDESTINA	TRECHO:	MISSÃO VELHA – PORTO DO PECÉM
SUB-TRECHO:	MVP-09		
OBJETO:	PROJETO EXECUTIVO – PROJETO GEOMÉTRICO	FOLHA:	19
ESCALA: H=1:2000 V=1:200	PLANTA E PERFIL km 400+729,951 ao 447+031,926	DESENHO Nº	FTN-MVP09-PJ4D-3483-001
		REV.	01