


ESCALA=1:50

ESCALA=1:50

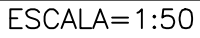

- 1_ DIMENSÕES EM CENTÍMETROS EXCETO ONDE INDICADO;
- 2_ CONCRETO ESTRUTURAL : $f_{ck} = 25 \text{ MPa}$
- 3_ OS ATERROS DEVERÃO SER COMPACTADOS SIMULTANEAMENTE NOS DOIS LADOS E COMPACTADOS COM ESPESURA NÃO SUPERIOR A 25 cm.
- 4_ DEPENDENDO DO COMPORTAMENTO DO ATERO, PODERÃO SER INCORPORADAS LAJES DE APROXIMAÇÃO ÀS OBRAS.
- 5_ TRECHO EM PIR, A TENSÃO NO TERRENO É ALIVIADA EM COMPARAÇÃO AO MESMO TRECHO SO ATERO.


[illegible]

ESCALA=1:50


ESCALA=1:50




ESCALA=1:50

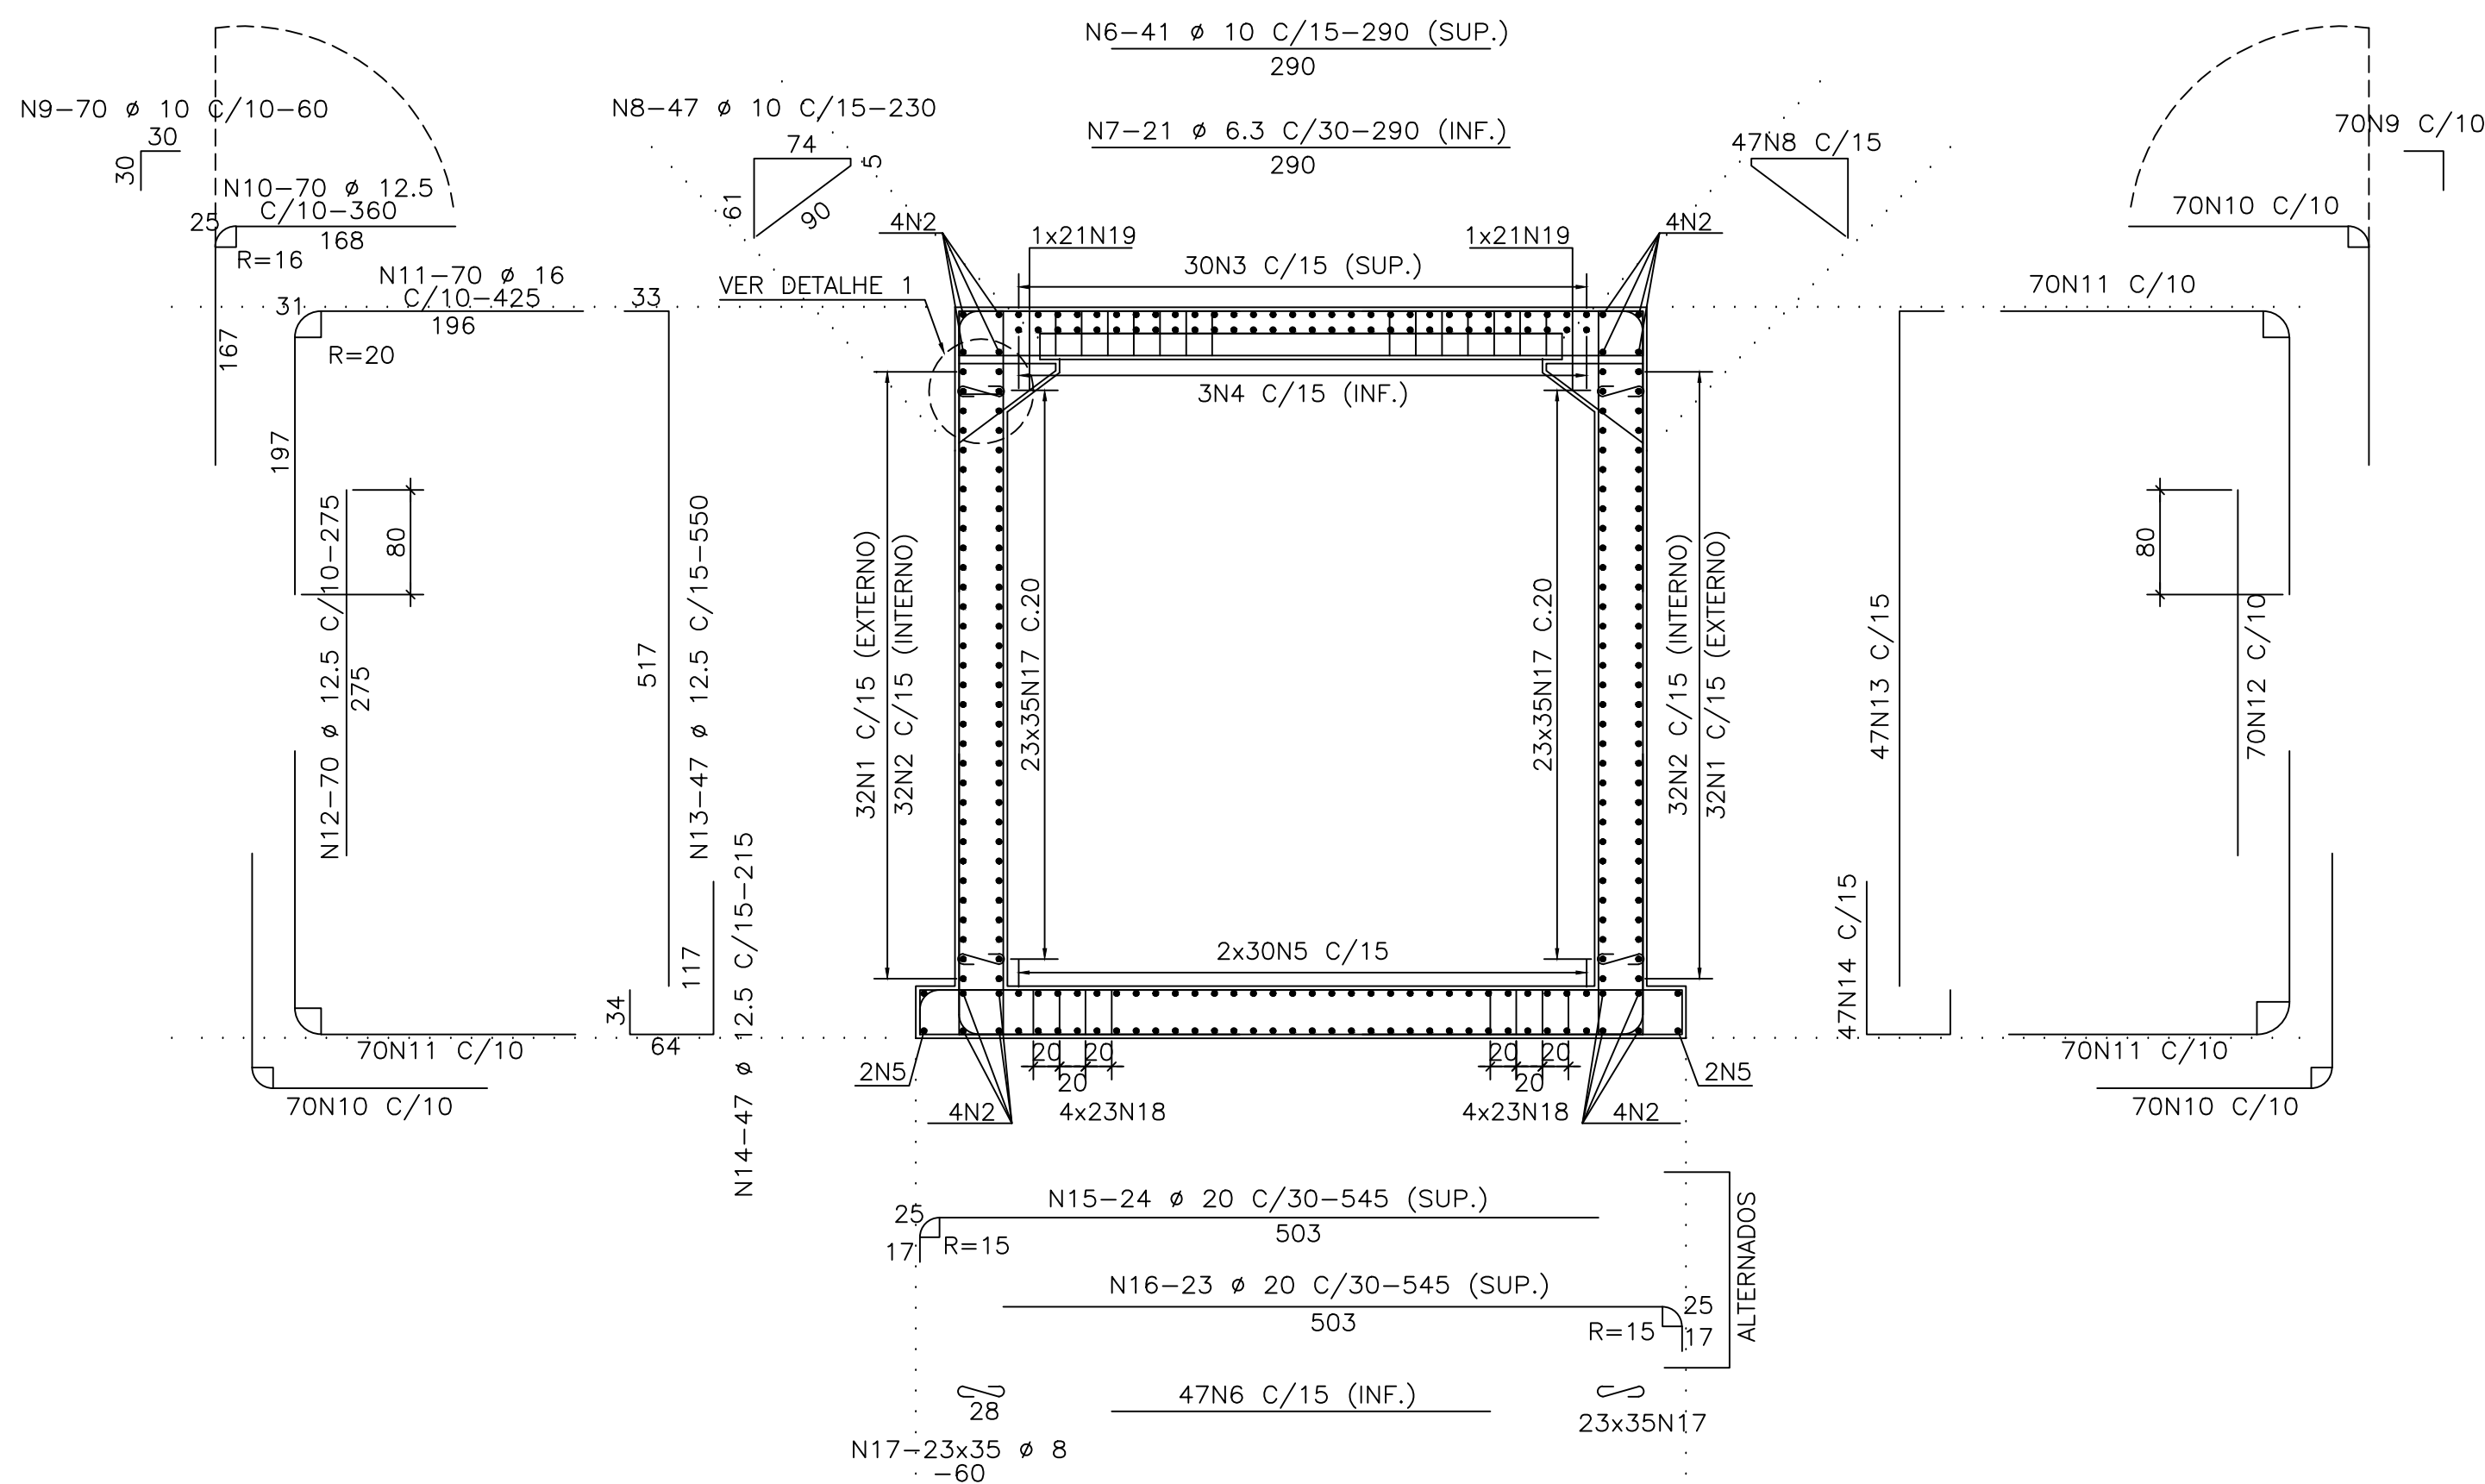


ESCALA=1:50

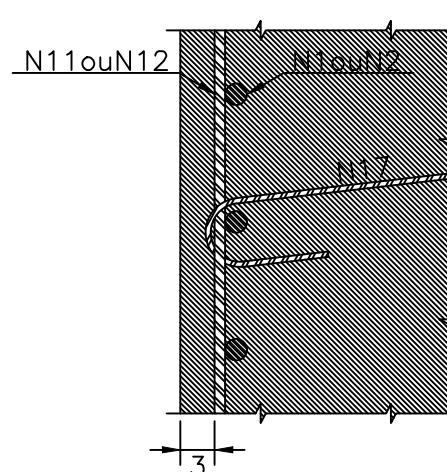

ESCALA=1:50

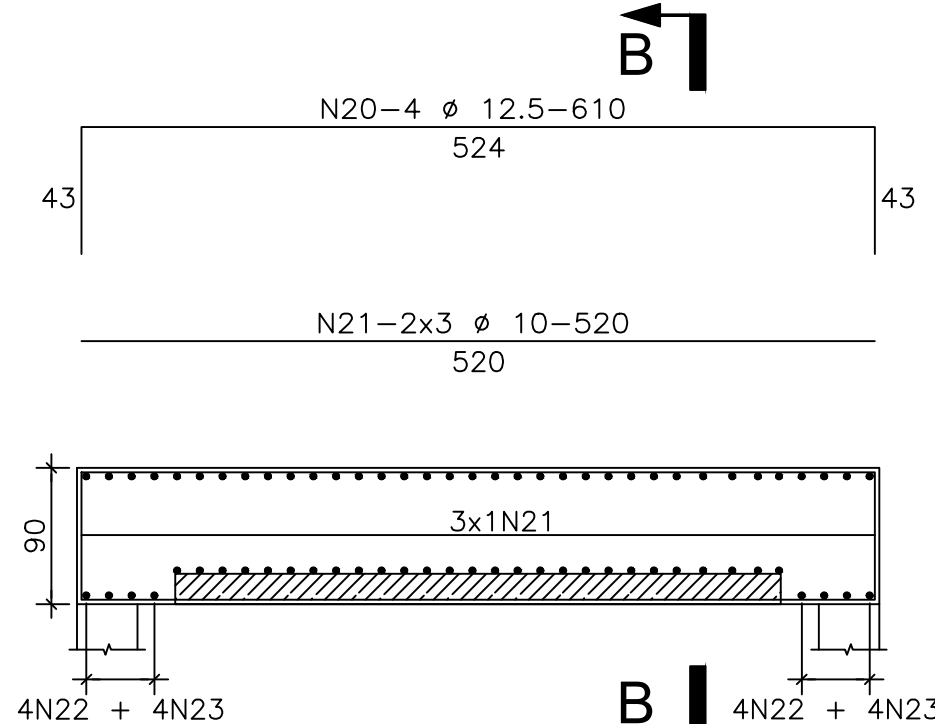

ESCALA=1:25

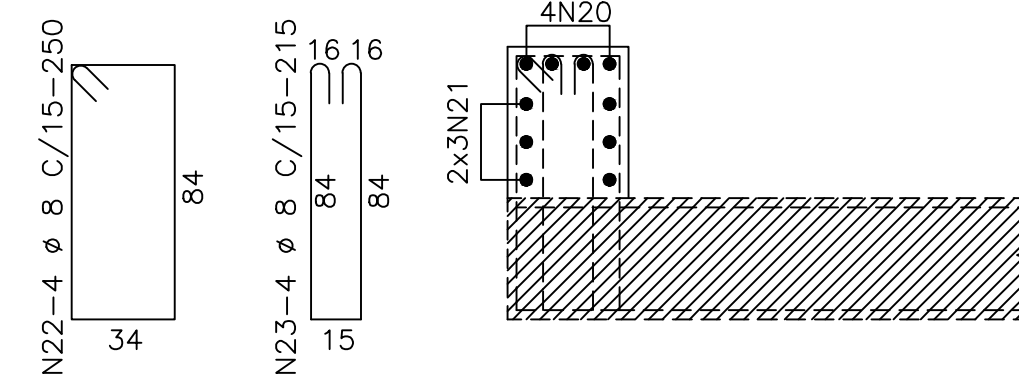

LISTA DE FERROS

RESUMO CA-50TOTAL PARA 1m DE PIR:

1175 kg

Ø	○	COMPRIMEN
---	---	-----------

RESUMO CA-50

Ø (mm)	COMPR (m)	PESO (kg)
8	37.20	15
10	62.40	39
12.5	48.80	47
TOTAL:		101

NOTAS

- 1_ DIMENSÕES EM CENTÍMETROS EXCETO ONDE INDICADO;
2_ CONCRETO ESTRUTURAL : $f_{ck} = 25 \text{ MPa}$
3_ OS ATERROS DEVERÃO SER COMPACTADOS SIMULTANEAMENTE NOS DOIS LADOS E COMPACTADOS COM ESPESURA NÃO SUPERIOR A 25 cm.
4_ DEPENDENDO DO COMPORTAMENTO DO ATERRO, PODERÃO SER INCORPORADAS LAJES DE APROXIMAÇÃO ÀS OBRAS.
5_ TRECHO EM PIR, A TENSÃO NO TERRENO É ALIVIADA EM COMPARAÇÃO AO MESMO TRECHO SOBO ATERRO.

6_ COBRIMENTO = 3cm
7_ AÇO CA-50

Nº	OBJETO	REV.	DESCRIÇÃO	DATA	ELABORAÇÃO	VERIFICAÇÃO	APROVAÇÃO
DOCUMENTOS DE REFERÊNCIA		00	EMIÇÃO INICIAL	25.07.11	ACFREIRE	TCFREIRE	GREY
			REVISÕES				



DESENHO:	TPRATA
PROJETO:	ACFREIRE
VERIFICAÇÃO:	TCFREIRE
RESP. TÉCNICO:	ACFREIRE
APROVADO:	GREY
DATA:	25.07.2011

TRANSNORDESTINA
Logistica S.A.

FERROVIA TRANSNORDESTINA

TRECHO: SPS - EMT E TS	SUBTRECHO: SPS - EM
PROJETO EXECUTIVO DE ADEQUAÇÃO	

PROJETO DE ADEQUAÇÃO DO SISTEMA VIÁRIO


PROJETO TÍPICO
PASSAGEM INTERIOR RESTRITA SIMPLES TÍPICA - ARMADURA

ESCALA:	CÓDIGO:	REV.:
---------	---------	-------


00	1/1
----	-----

ESCALA=1:25


ESCALA=1:25

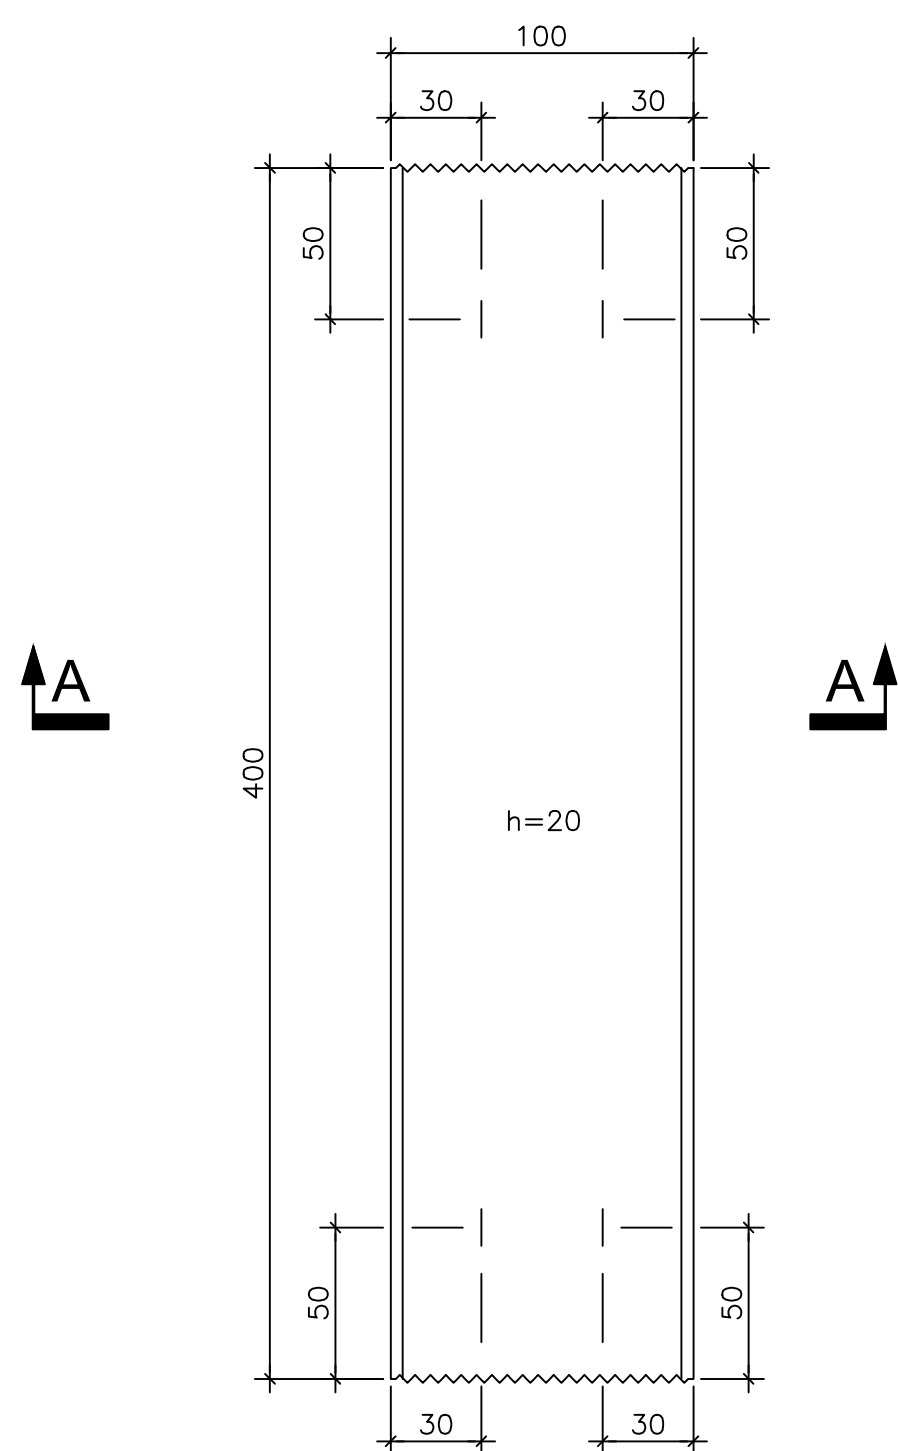


ESCALA=1:12.5

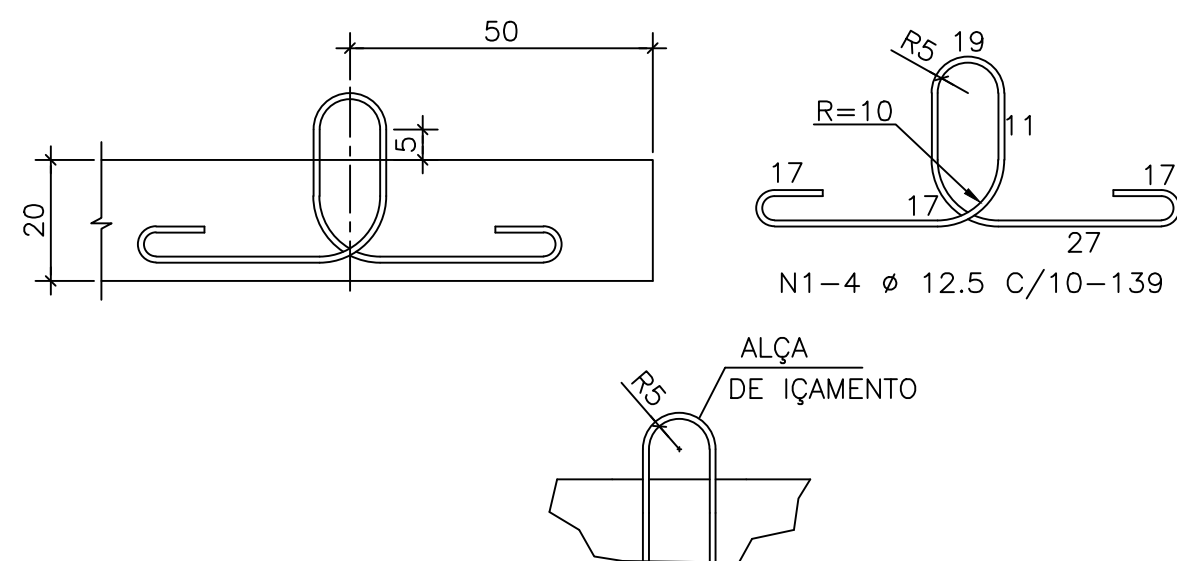


ESCALA=1:12.5

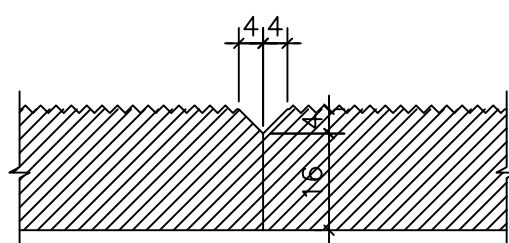


ESCALA=1:12.5

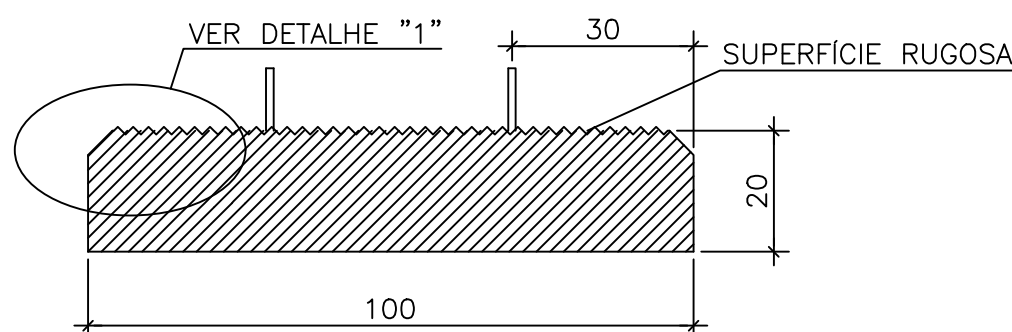


ESCALA=1:25

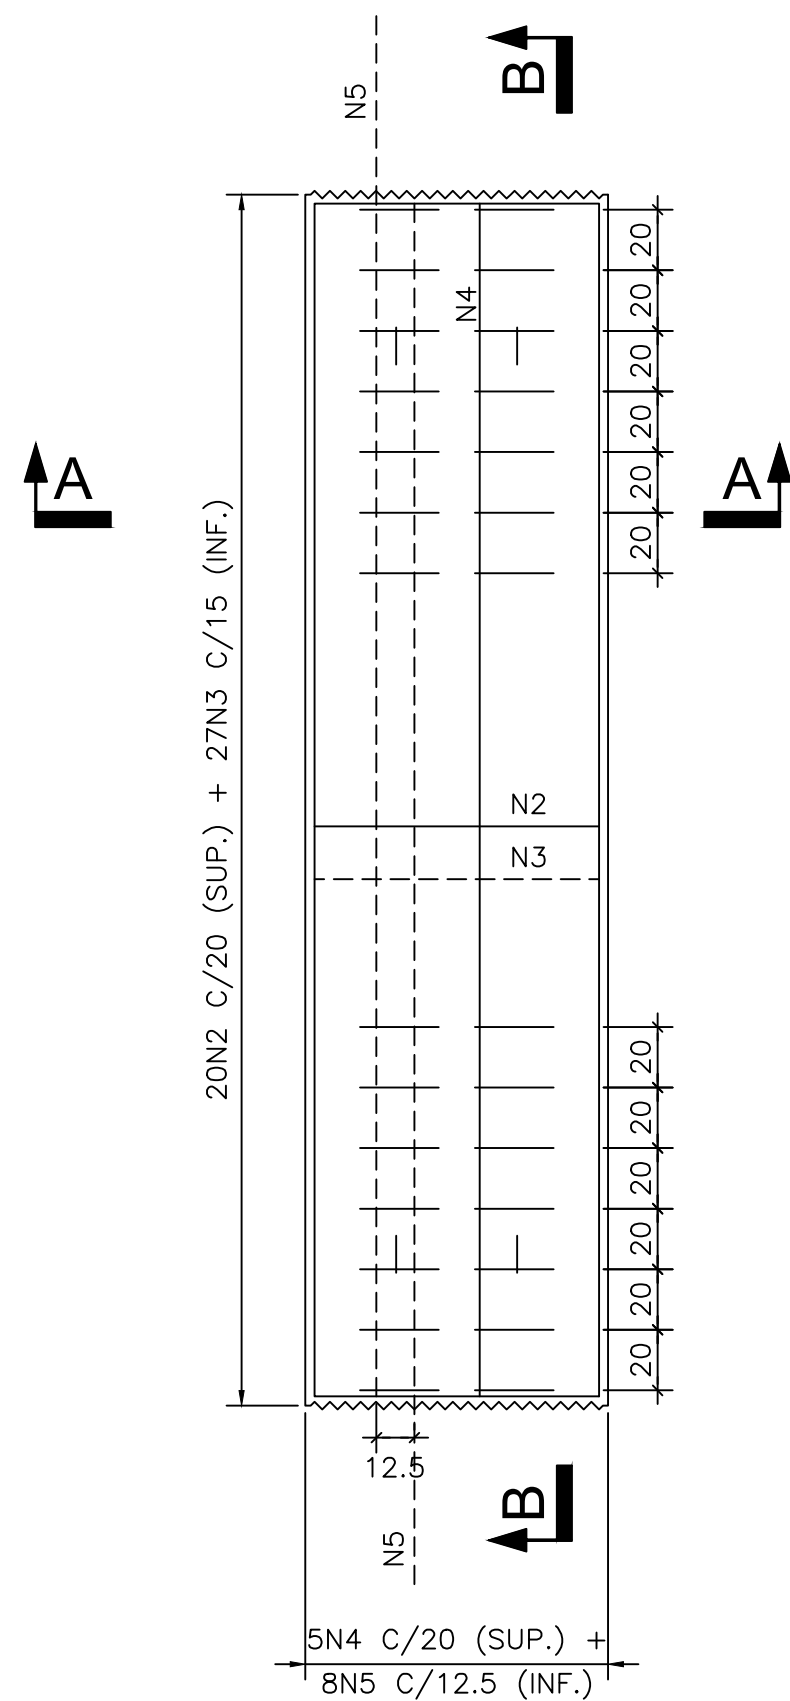

ESCALA=1:12.5

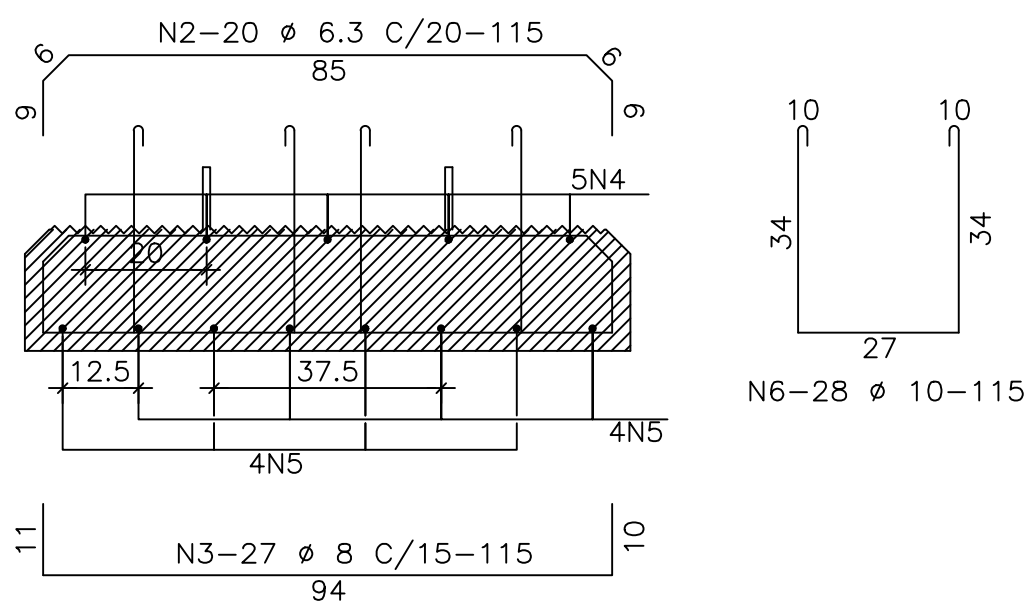

ESCALA=1:25

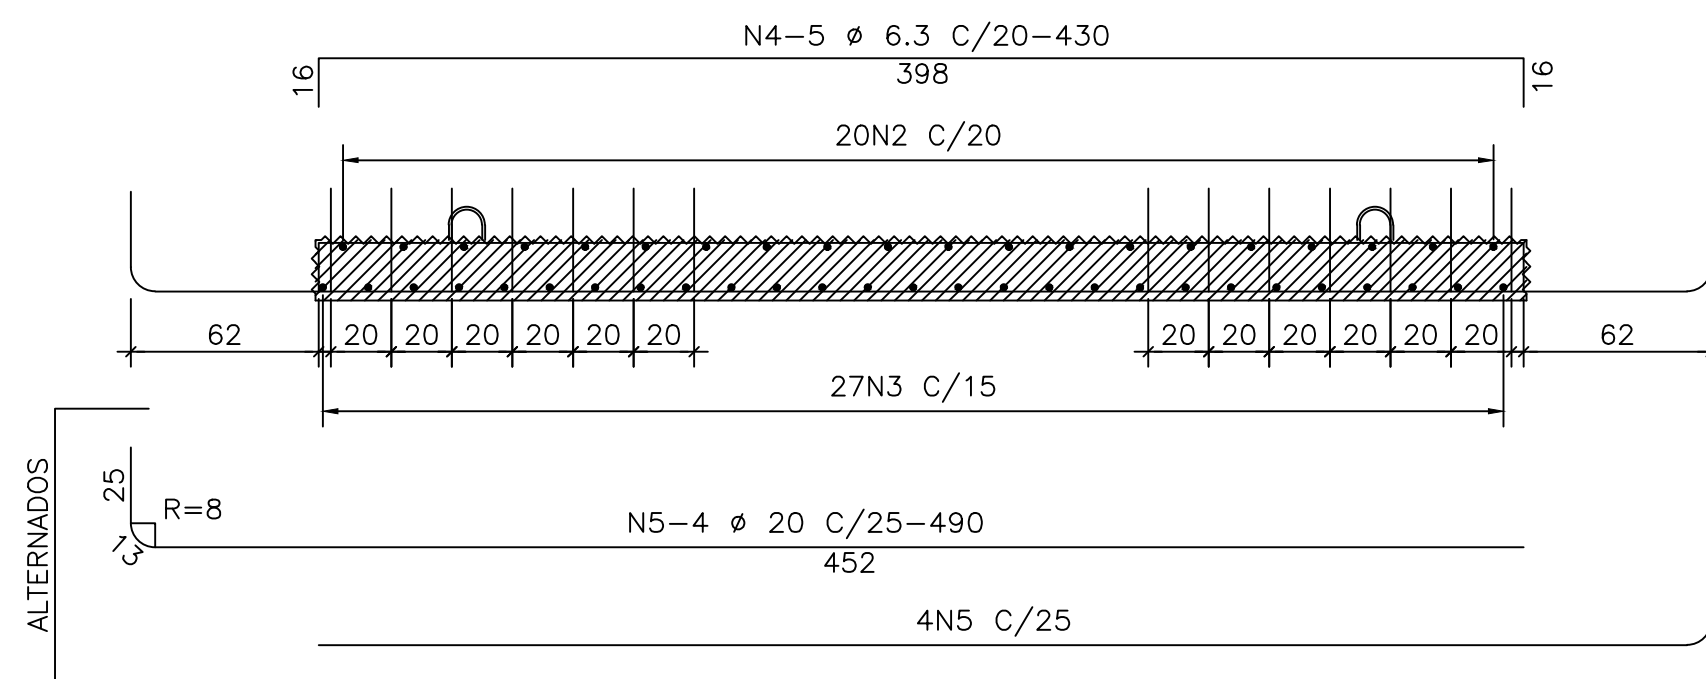


N	Ø (mm)	Q	COMPRIMENTO	
			UNIT.(cm)	TOTAL(m)
1	12.5	4	139	5.56
2	6.3	20	115	23.00
3	8	27	115	31.05
4	6.3	5	430	21.50
5	20	8	490	39.20
6	10	28	115	32.20


RESUMO CA-50		
Ø (mm)	COMPR (m)	PESO (kg)
6.3	44.50	11
8	31.05	12
10	32.20	20
20	39.20	97
TOTAL:		140

RESUMO CA-25		
Ø (mm)	COMPR (m)	PESO (kg)
12.5	5.56	5
TOTAL:		5


ESCALA=1:25

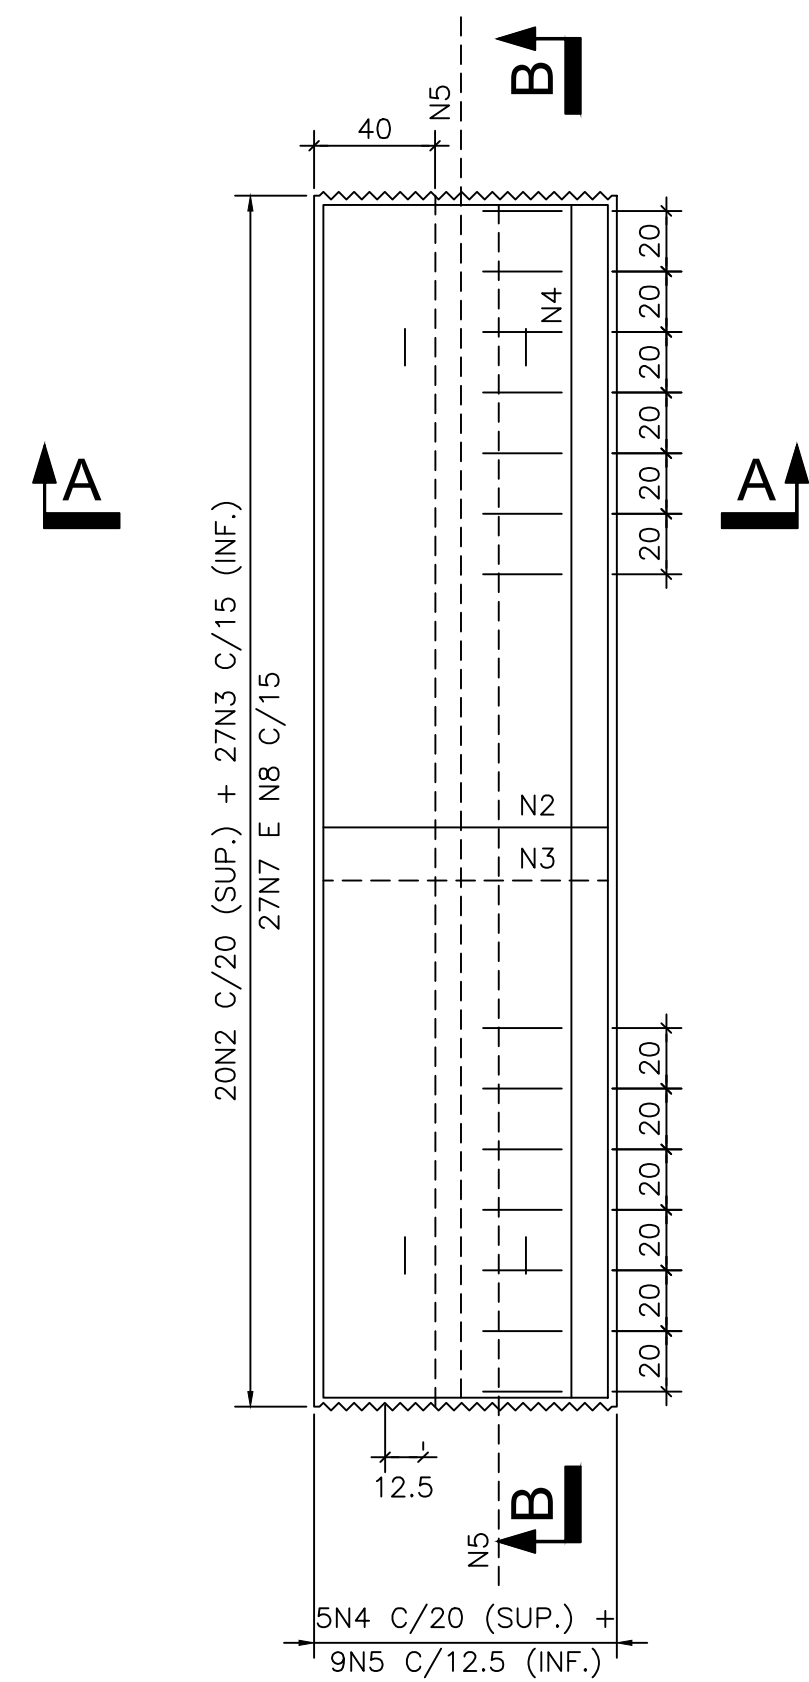

ESCALA=1:12.5

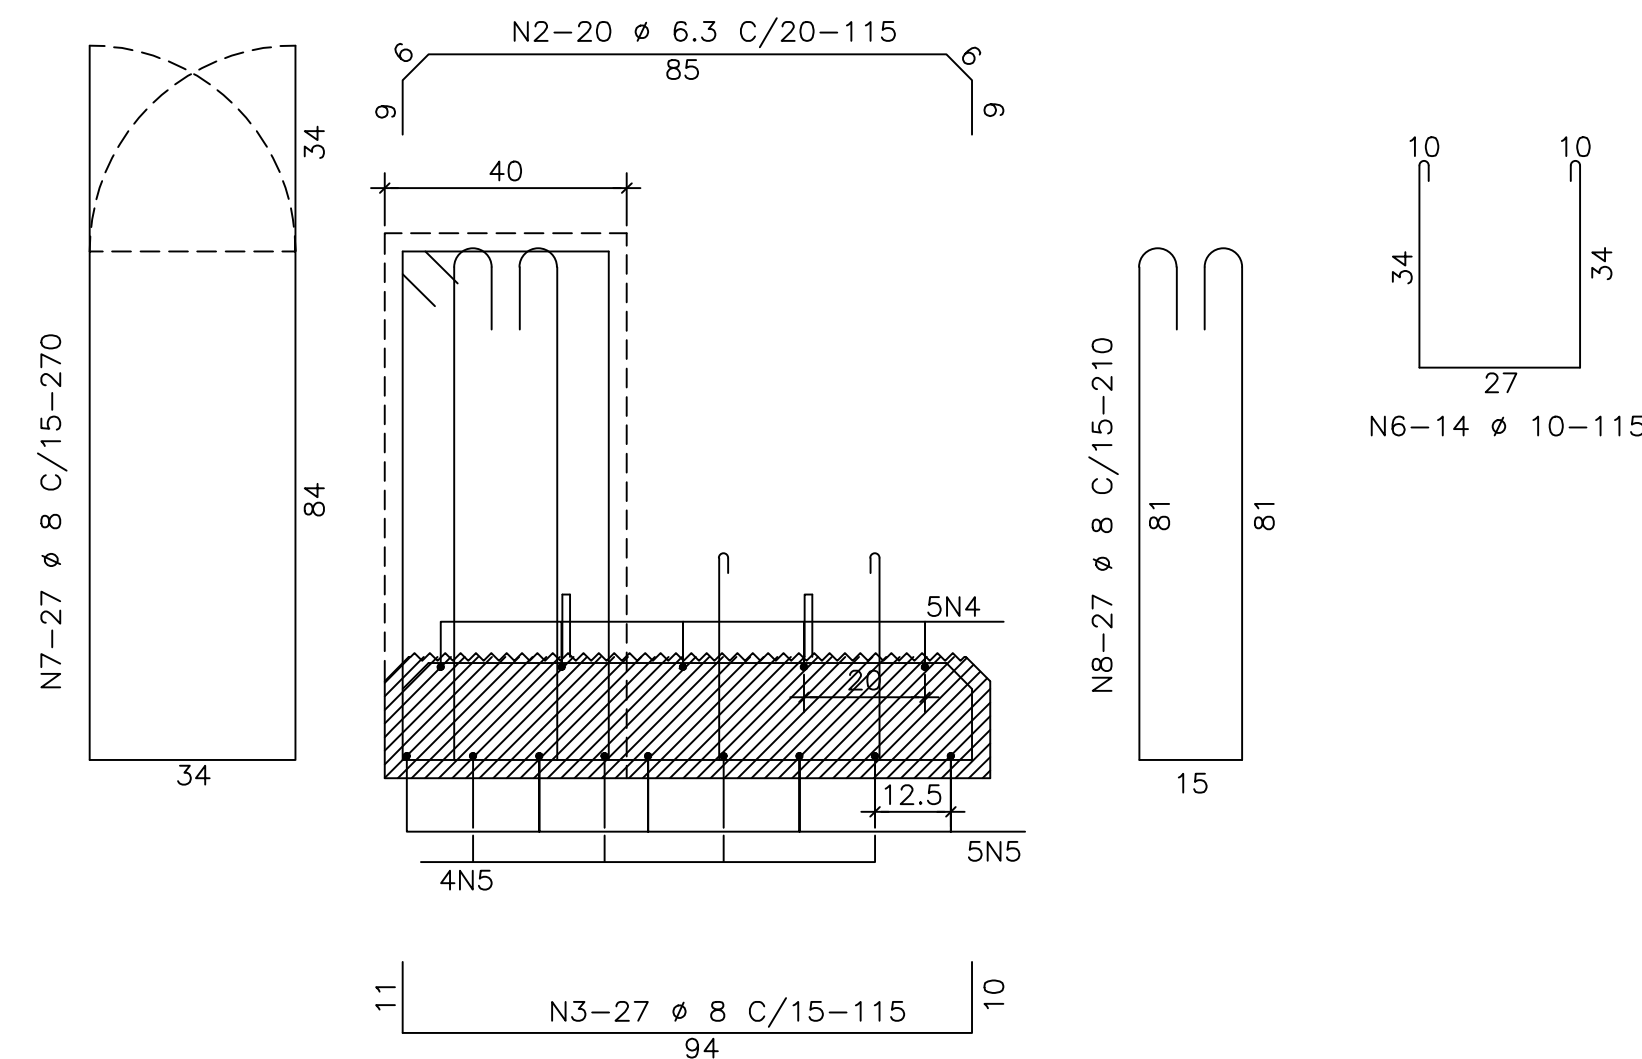

ESCALA=1:25

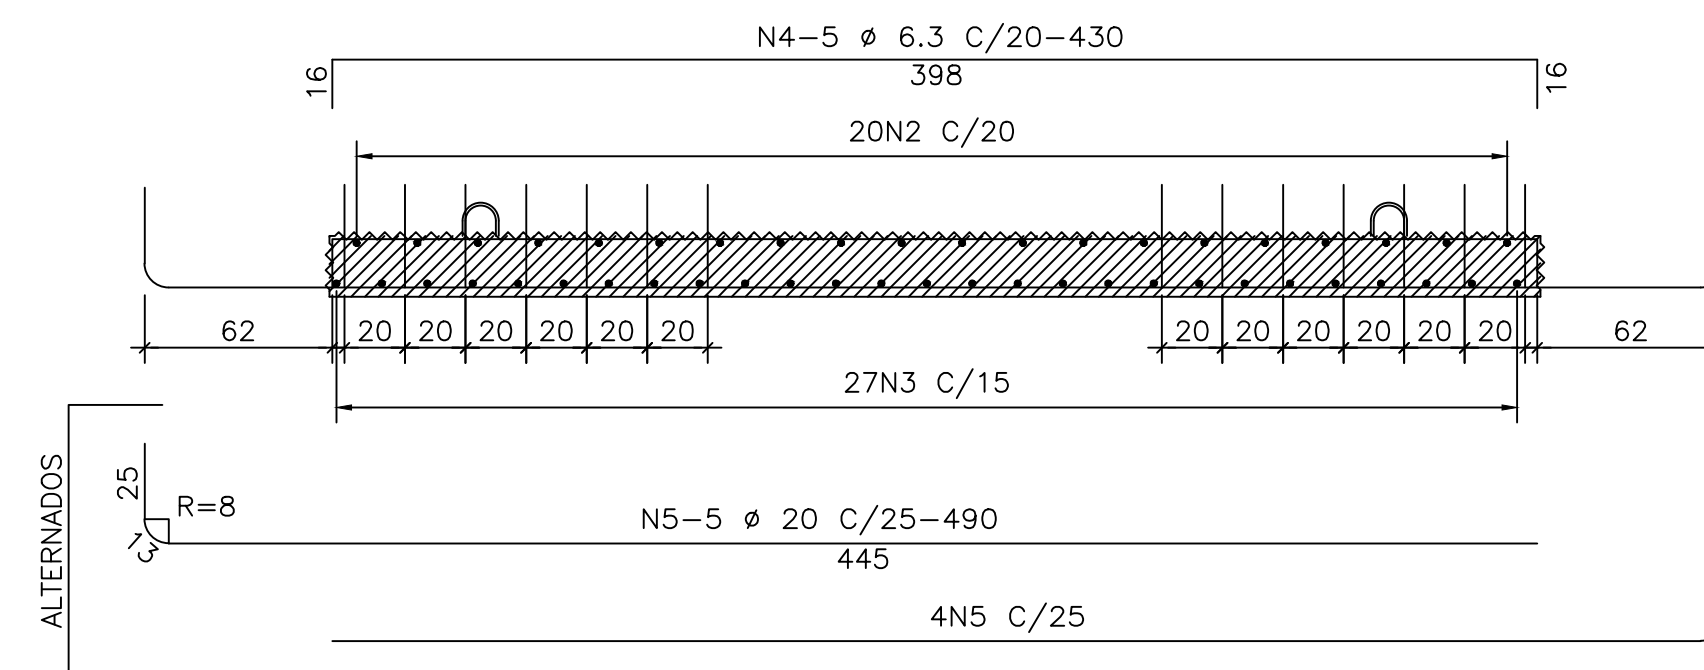

N	$\emptyset$ (mm)	Q	COMPRIMENTO	
			UNIT.(cm)	TOTAL(m)
1	12.5	4	139	5.56
2	6.3	20	115	23.00
3	8	27	115	31.05
4	6.3	5	430	21.50
5	20	9	490	44.10
6	10	14	115	16.10
7	8	27	270	72.90
8	8	27	210	56.70

RESUMO CA-50		
Ø (mm)	COMPR (m)	PESO (kg)
6.3	44.50	11
8	160.65	64
10	16.10	10
20	44.10	109
TOTAL:		194

RESUMO CA-25		
Ø (mm)	COMPR (m)	PESO (kg)
12.5	5.56	5
TOTAL:		5

[illegible]

ESCALA=1:50

ESCALA=1:50



ESCALA=1:50



ESCALA=1:50



1. DIMENSÕES EM CENTÍMETROS EXCETO ONDE INDICADO;
2. CONCRETO ESTRUTURAL : $f_{ck} = 25 \text{ MPa}$
3. OS ATERROS DEVERÃO SER COMPACTADOS SIMULTANEAMENTE NOS DOIS LADOS E COMPACTADOS COM ESPESURA NÃO SUPERIOR A 25 cm.
4. DEPENDENDO DO COMPORTAMENTO DO ATERRO, PODERÃO SER INCORPORADAS LAJES DE APROXIMAÇÃO ÀS OBRAS.
5. TRECHO EM PIR, A TENSÃO NO TERRENO É ALIVIADA EM COMPARAÇÃO AO MESMO TRECHO SO ATERRO.


REV.: 00	FOLHA: 1/1
----------	------------



ESCALA=1:50





ESCALA=1:50

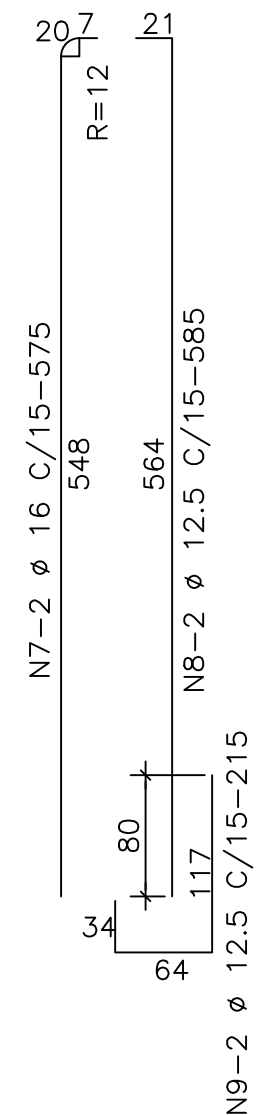

ESCALA=1:50



TOTAL PARA 3 PIR'S	
TOTAL(x3):	21.918

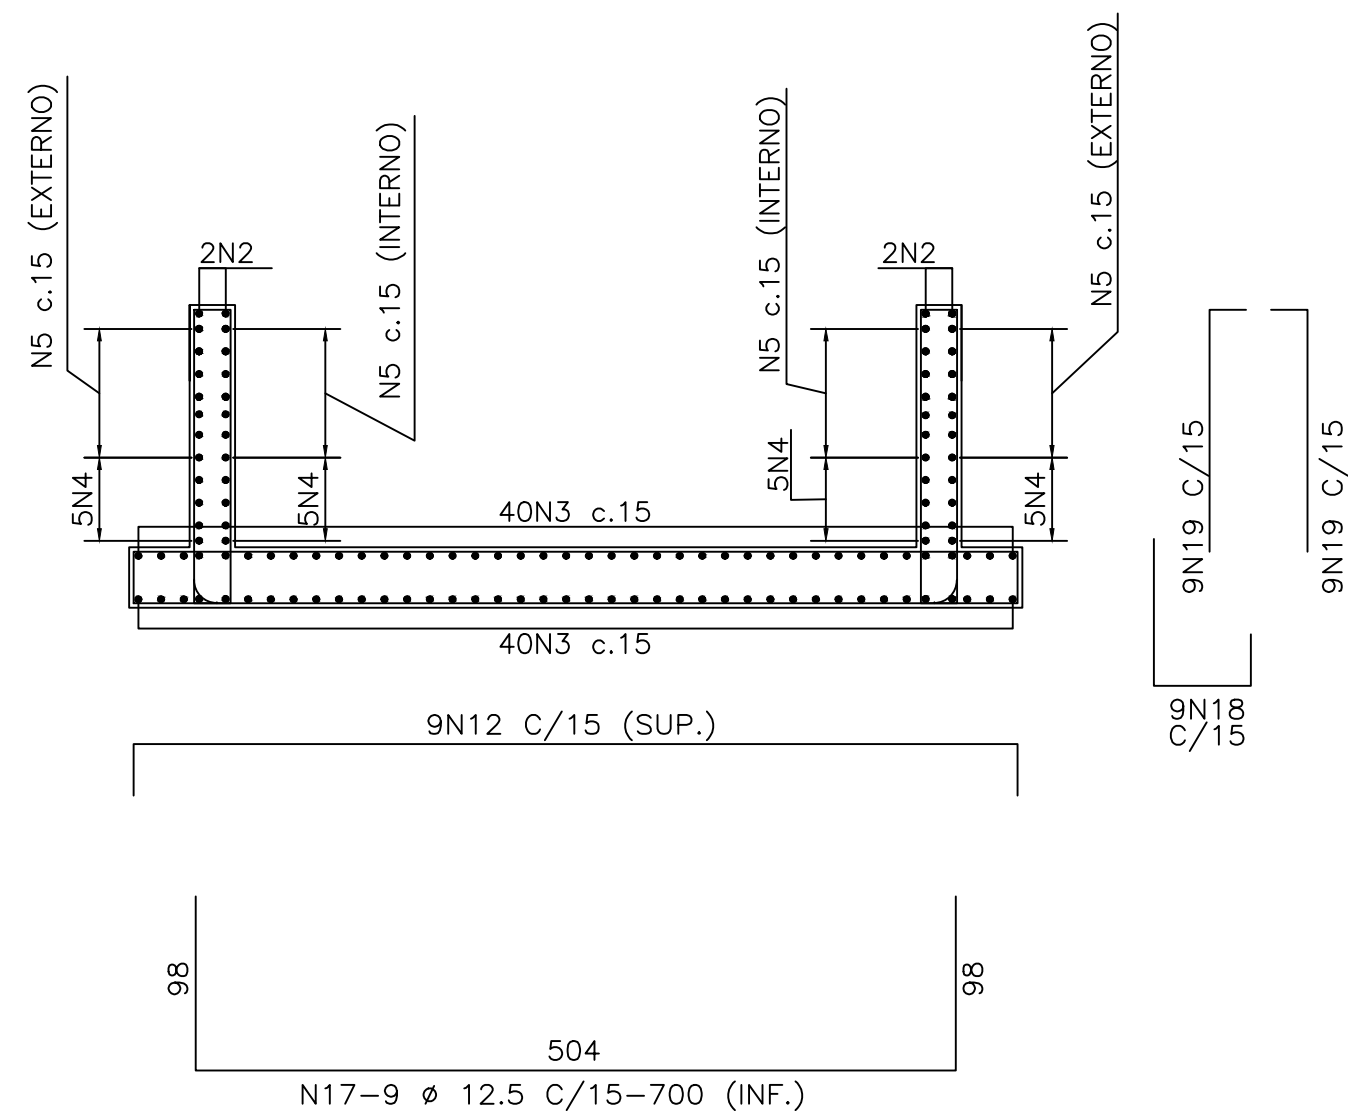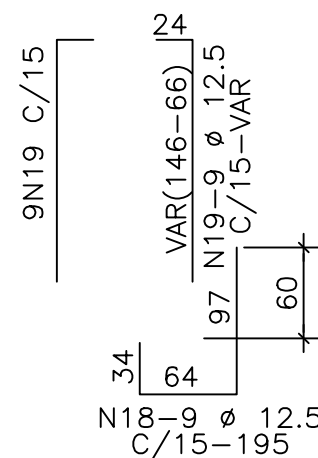

1_ DIMENSÕES EM CENTÍMETROS EXCETO ONDE INDICADO;
2_ CONCRETO ESTRUTURAL : $f_{ck} = 25 \text{ MPa}$
3_ OS ATERROS DEVERÃO SER COMPACTADOS SIMULTANEAMENTE NOS DOIS LADOS
E COMPACTADOS COM ESPESURA NÃO SUPERIOR A 25 cm.
4_ COBRIMENTO = 3cm

Nº	OBJETO	REV.	DESCRIÇÃO	DATA	ELABORAÇÃO	VERIFICAÇÃO	APROVAÇÃO
DOCUMENTOS DE REFERÊNCIA		00	EMIÇÃO INICIAL	17.08.11	ACFREIRE	TCFREIRE	GREY
			REVISÕES				



**BETON
STAHL**
Engenharia Ltda

TRANSNORDESTINA
Logística S.A.

FERROVIA TRANSNORDESTINA

TRECHO: SPS - EMT E TS

PROJETO EXECUTIVO DE ADEQUAÇÃO


PROJETO DE ADEQUAÇÃO DO SISTEMA VIÁRIO
PROJETO TÍPICO

PASSAGEM INFERIOR RESTRITA TÍPICA - ARMADURA DAS


ESCALA:	CÓDIGO:	REV.:	FOLHA:
INDICADA	FTN-GERAL-DE2B-1458-049	00	1

REV.: 00	FOLHA: 1/
----------	-----------


ESCALA=1:25

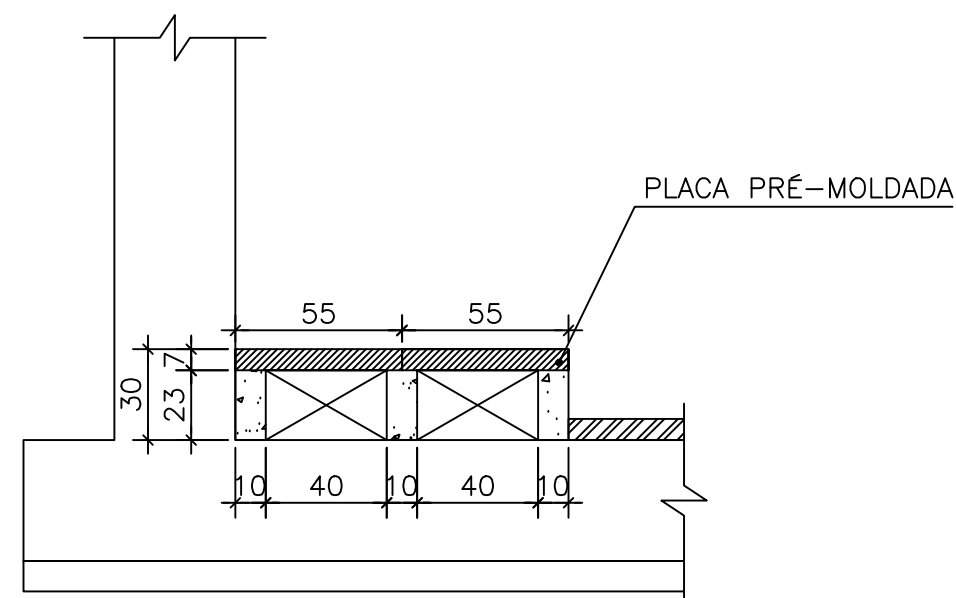


ESCALA=1:25

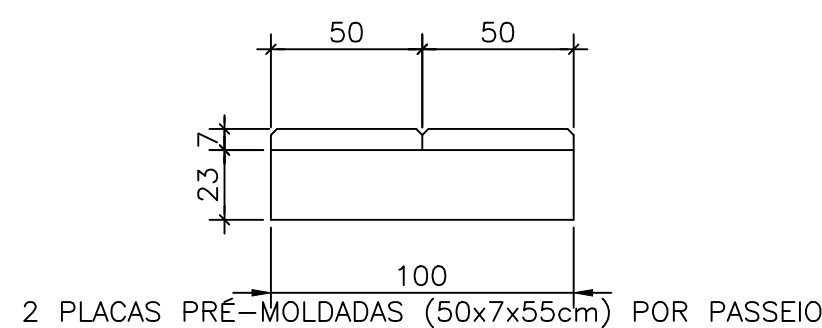


ESCALA=1:25

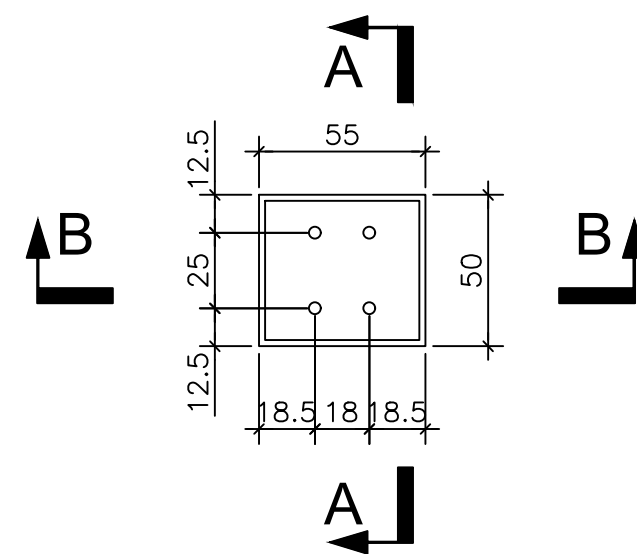


ESCALA=1:12.5

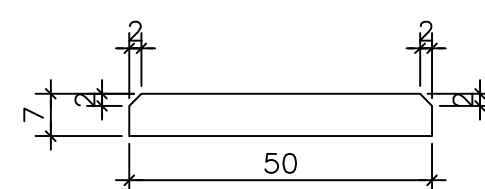


ESCALA=1:12.5

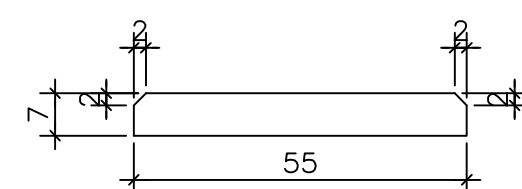

ESCALA=1:12.5

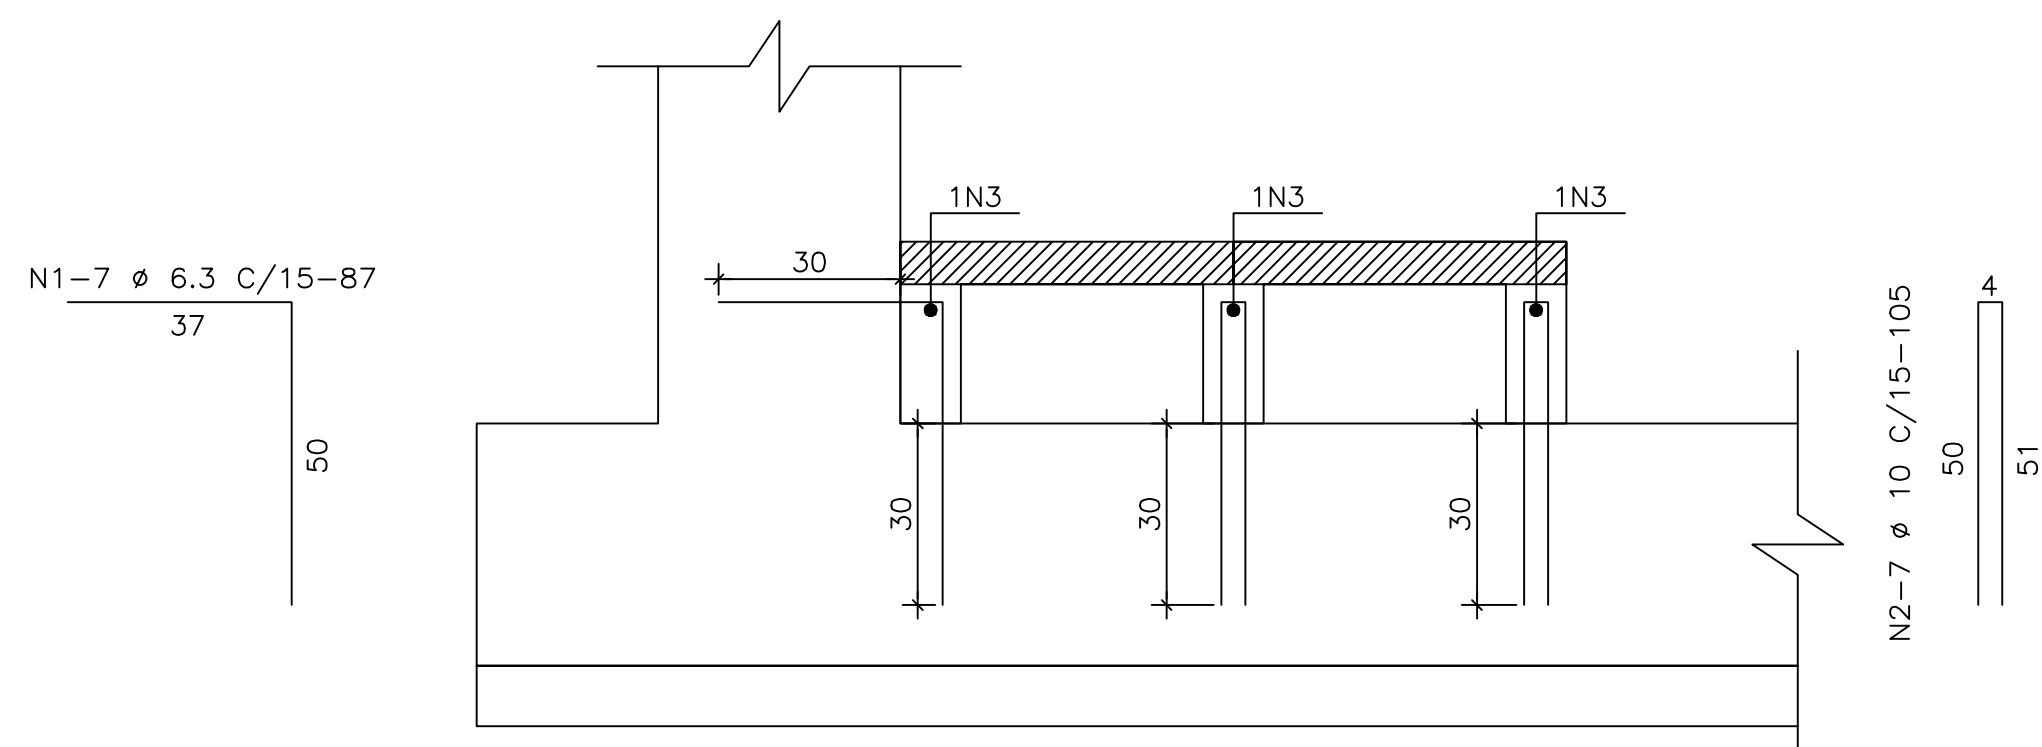


FSCAI A=1:12.5

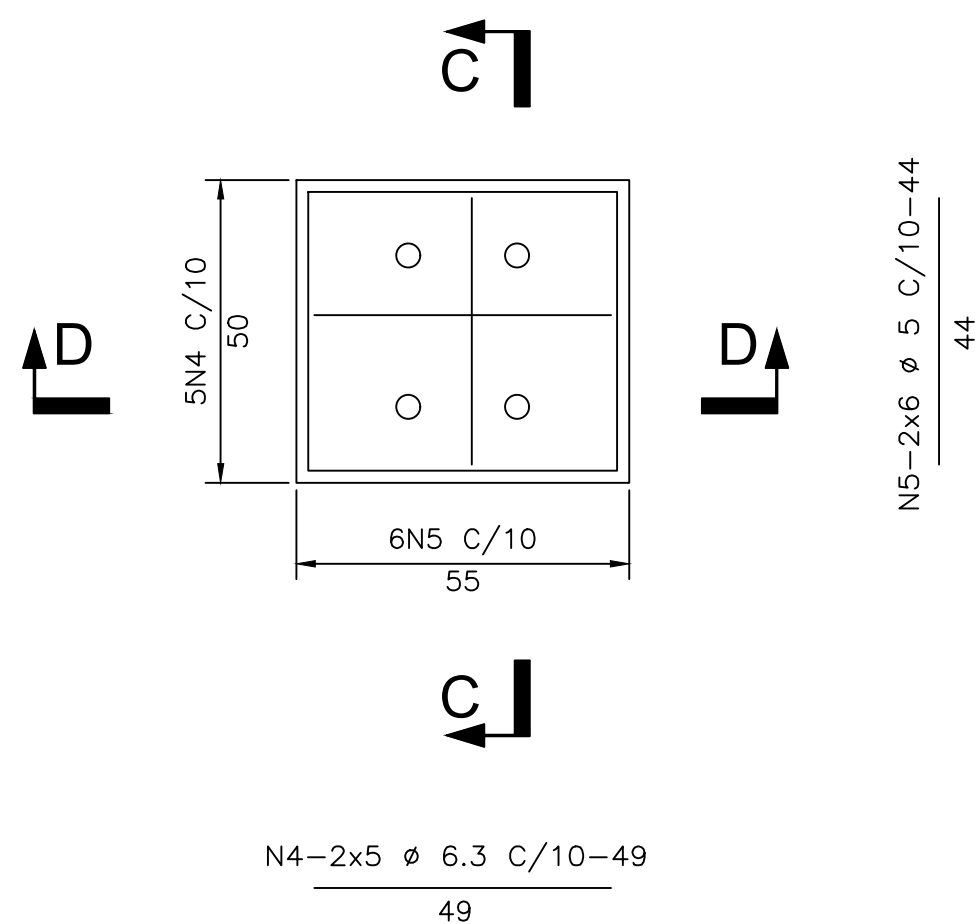


N	Ø (mm)	Q	COMPRIMENTO	
			UNIT.(cm)	TOTAL(m)
1	6.3	7	87	6.09
2	10	7	105	7.35
3	10	3	CORRIDO	3.84
4	6.3	20		49
5	5	24	44	10.56

RESUMO CA-50		
Ø (mm)	COMPR (m)	PESO (kg)
5	10.56	2
6.3	15.89	4
10	11.19	7
TOTAL:		13


ESCALA=1:50

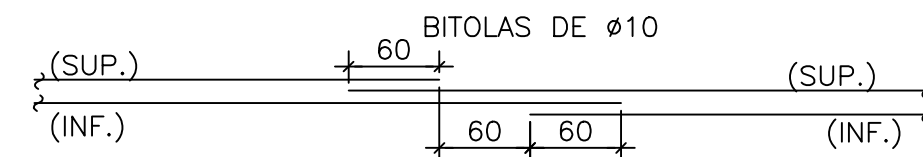


ESCALA=1:25

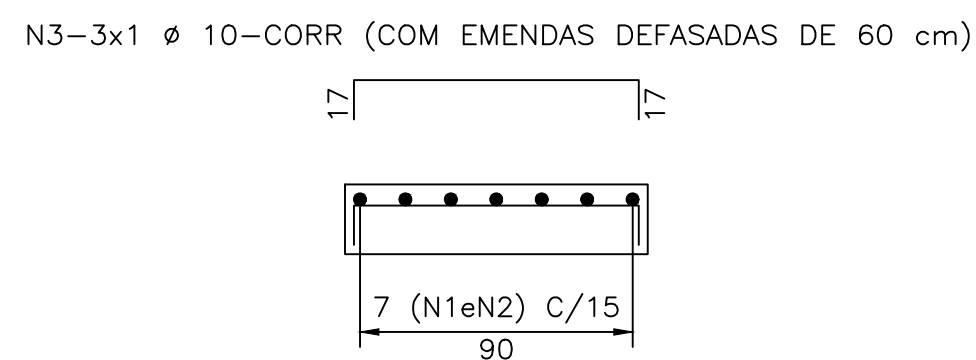

S/ESCALA

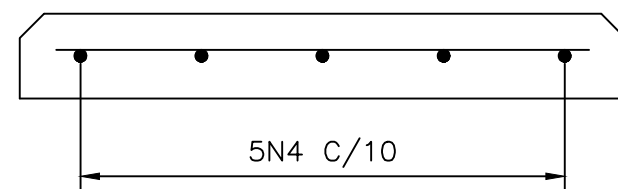

S/ESCALA

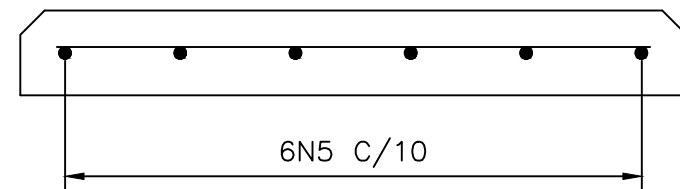

1_ DIMENSÕES EM CENTÍMETROS EXCETO ONDE INDICADO;
2_ CONCRETO ESTRUTURAL : fck= 25 MPa
3_ OS ATERROS DEVERÃO SER COMPACTADOS SIMULTANEAMENTE NOS DOIS LADOS
E COMPACTADOS COM ESPESSURA NÃO SUPERIOR A 25 cm.
4_ COBRIMENTO = 3cm
5_ ESTE DESENHO PODE SER UTILIZADO PARA TODAS AS INCLINAÇÕES.

Nº	OBJETO	REV.	DESCRIÇÃO	DATA	ELABORAÇÃO	VERIFICAÇÃO	APROVAÇÃO
DOCUMENTOS DE REFERÊNCIA		00	EMISSION INICIAL	06.09.11	ACFREIRE	TCFREIRE	GREY
			REVISÕES				

 SETON S.A. Engenharia Ltda	TRANSNORDESTINA <i>Logística S.A.</i>		
	FERROVIA TRANSNORDESTINA		
	DESENHO: TP/RTA	TRECHO: SPS - EMT E TS	SUBTRECHO: SPS - EMT E TS
	PROJETO: ACFRRE	PROJETO EXECUTIVO DE ADEQUAÇÃO	
	VERIFICAÇÃO: TCFRRE	PROJETO DE ADEQUAÇÃO DO SISTEMA VIÁRIO	
RESP. TÉCNICO: ACFRRE	PROJETO TIPO		
APROVAÇÃO: GREY	PASSAGEM INFERIOR RESTRITA SIMPLES TIPO - FORMA E ARMADURA DOS PASSOS		
DATA: 06.09.2011	ESCALA: INDICADA	CÓDIGO: FTM-GERAL-DE28-1458-055	REV: 00 FOLHA 1/1