

ESCALA=1:50

ESCALA=1:50



1. DIMENSÕES EM CENTÍMETROS EXCETO ONDE INDICADO;
2. CONCRETO ESTRUTURAL : $f_{ck} = 25 \text{ MPa}$
3. OS ATERROS DEVERÃO SER COMPACTADOS SIMULTANEAMENTE NOS DOIS LADOS E COMPACTADOS COM ESPESURA NÃO SUPERIOR A 25 cm.
4. DEPENDENDO DO COMPORTAMENTO DO ATERRO, PODERÃO SER INCORPORADAS LAJES DE APROXIMAÇÃO ÀS OBRAS.
5. TRECHO EM PIR, A TENSÃO NO TERRENO É ALIVIADA EM COMPARAÇÃO AO MESMO TRECHO SO ATERRO.


[illegible]

ESCALA=1:50

ESCALA=1:50




ESCALA=1:50

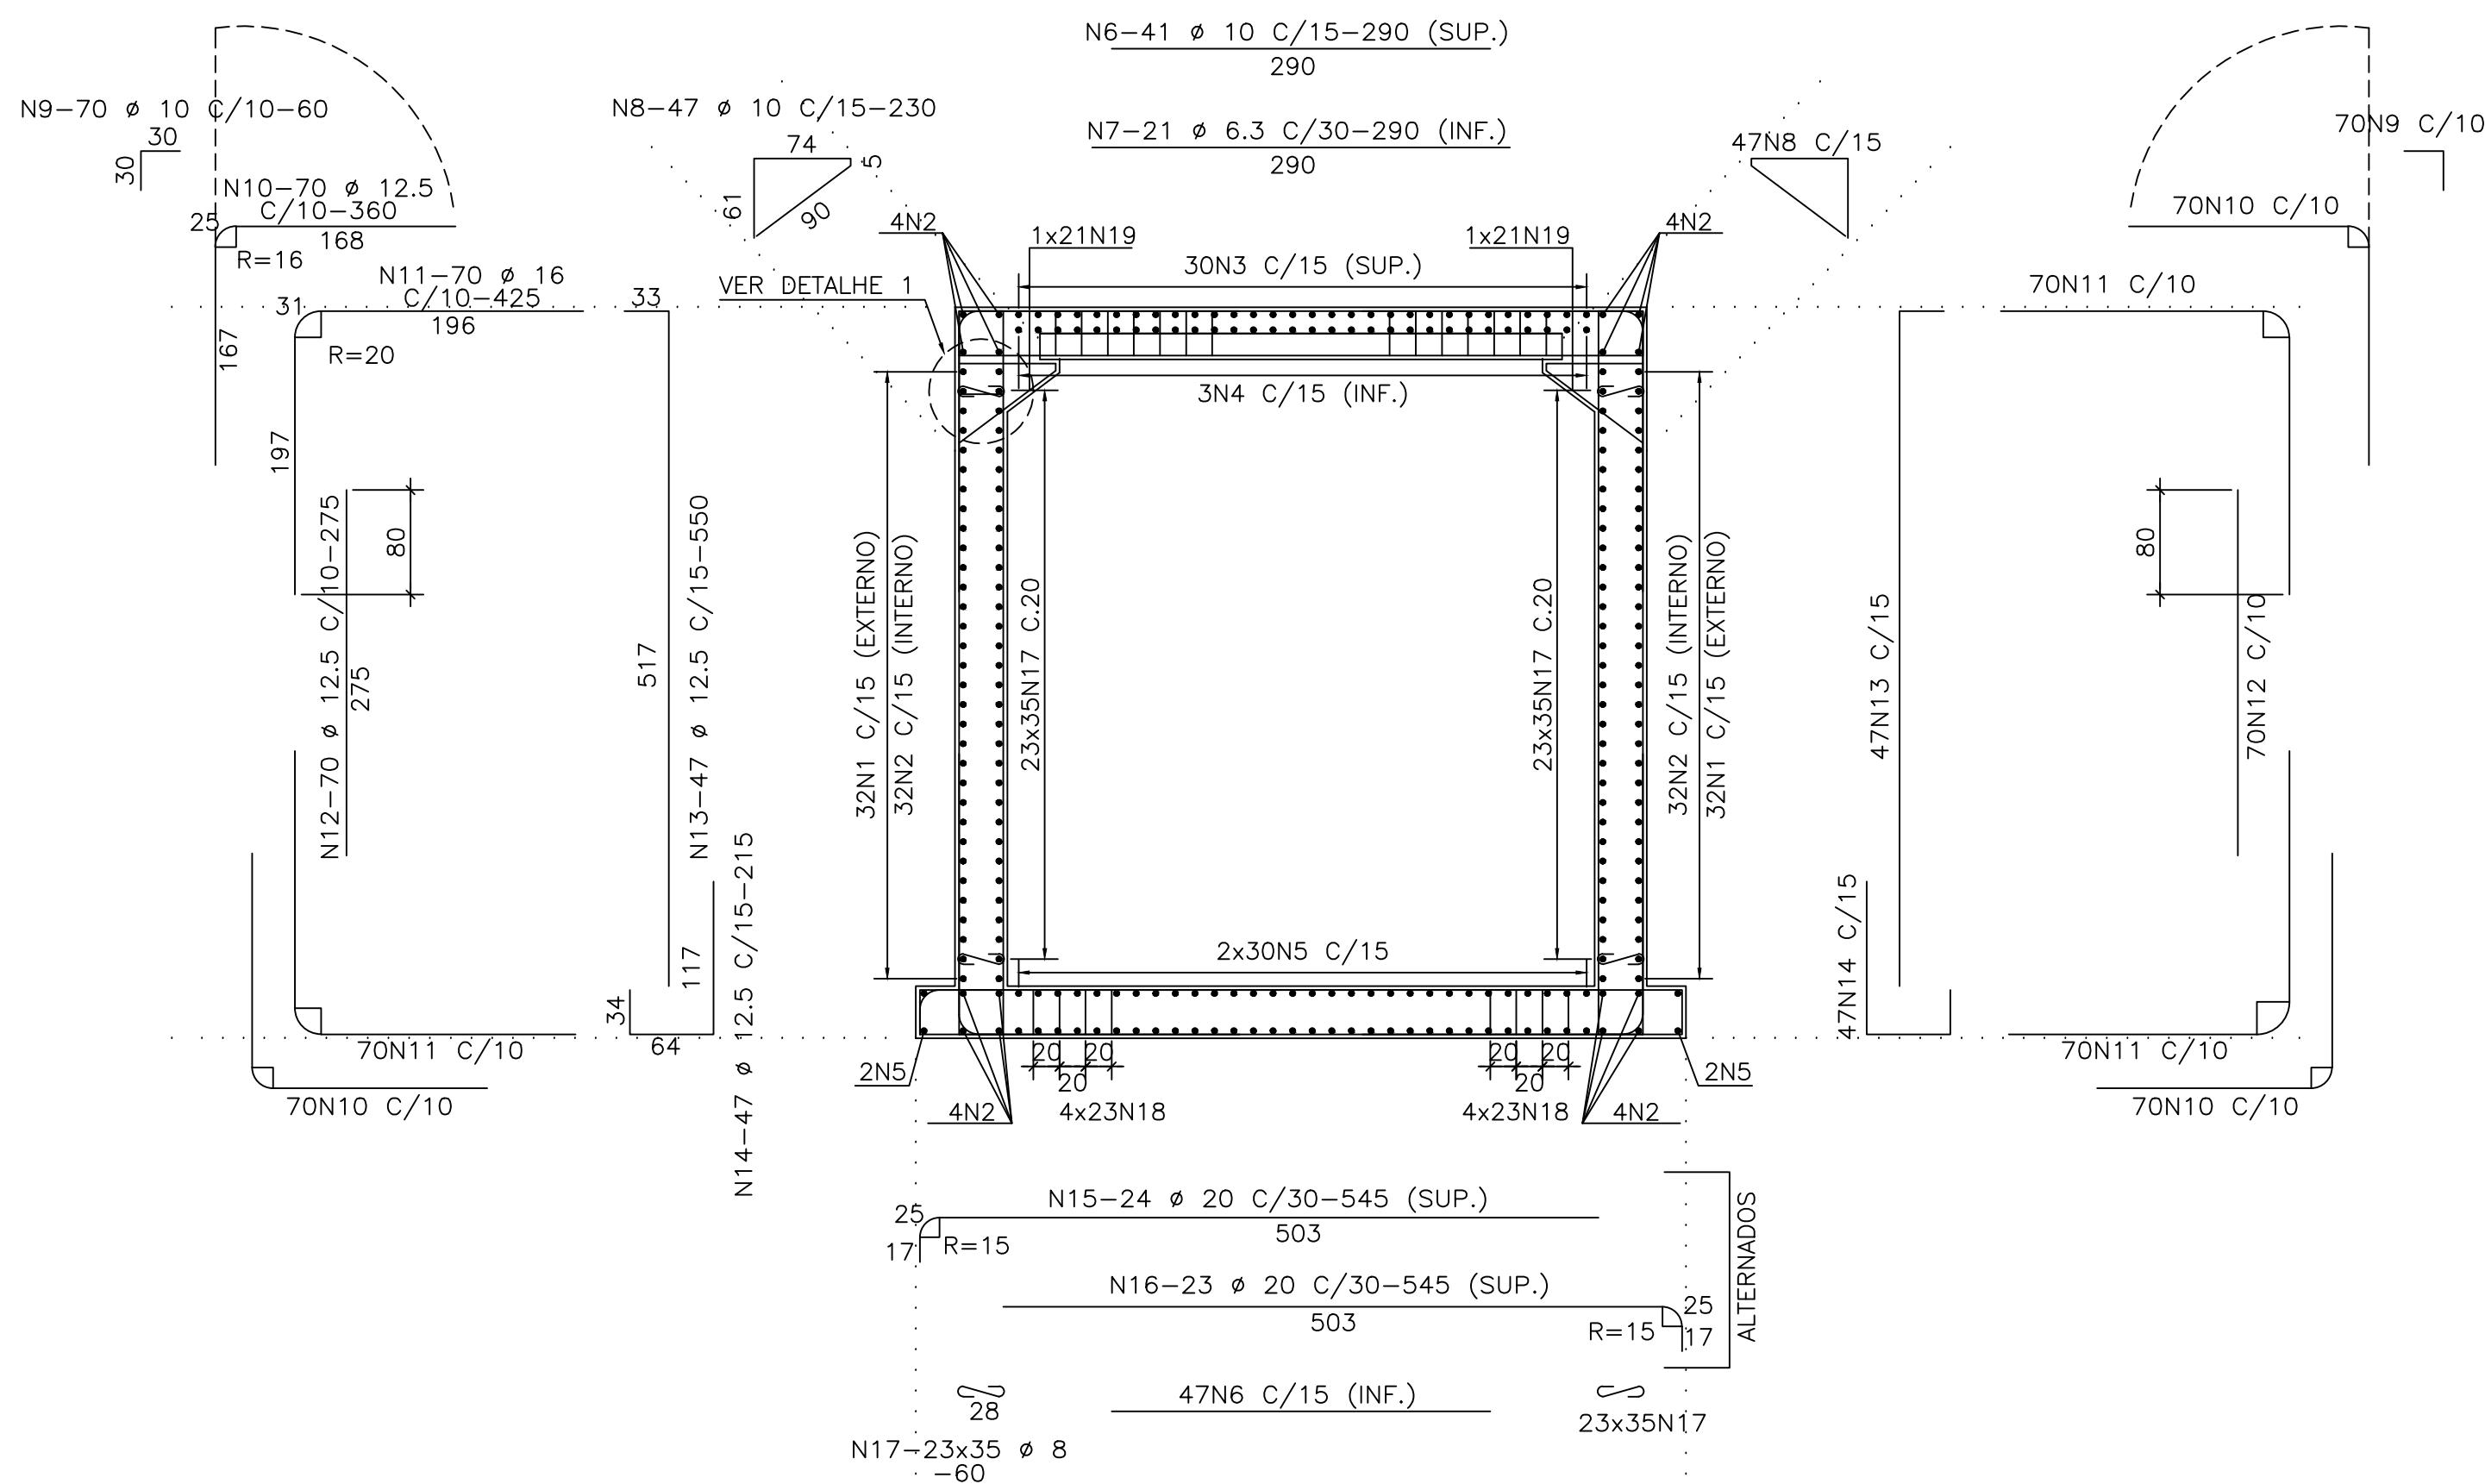

ESCALA=1:50



ESCALA=1:25

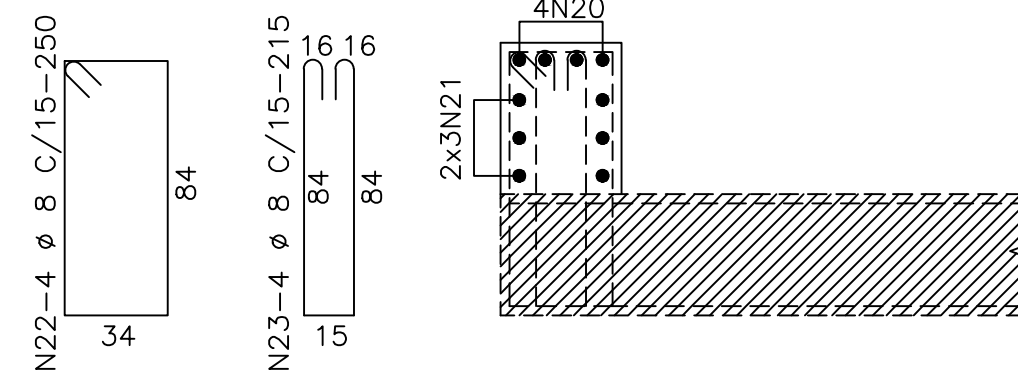

LISTA DE FERROS

RESUMO CA-50		
Ø (mm)	COMPR (m)	PESO (kg)
6.3	60.90	15
8	966.00	382
10	834.20	515
12.5	3230.50	3111
16	1397.00	2205
20	808.15	1993
TOTAL:		8221

LISTA DE FERROS P/2 VIGAS

RESUMO CA-50		
Ø (mm)	COMPR (m)	PESO (kg)
8	37.20	15
10	62.40	39
12.5	48.80	47
TOTAL:		101

RESUMO CA-50

Ø (mm)	COMPR (m)	PESO (kg)
8	37.20	15
10	62.40	39
12.5	48.80	47
TOTAL:		101

NOTAS

- 1_ DIMENSÕES EM CENTÍMETROS EXCETO ONDE INDICADO;
- 2_ CONCRETO ESTRUTURAL : fck= 25 MPa
- 3_ OS ATERROS DEVERÃO SER COMPACTADOS SIMULTANEAMENTE NOS DOIS LADOS E COMPACTADOS COM ESPESURA NÃO SUPERIOR A 25 cm.
- 4_ DEPENDENDO DO COMPORTAMENTO DO ATERRO, PODERÃO SER INCORPORADAS LAJES DE APROXIMAÇÃO ÀS OBRAS.
- 5_ TRECHO EM PIR, A TENSÃO NO TERRENO É ALIVIADA EM COMPARAÇÃO AO MESMO TRECHO SO ATERRO.

6_ COBRIMENTO = 3cm
7_ AÇO CA-50

Nº	OBJETO	REV.	DESCRIÇÃO	DATA	ELABORAÇÃO	VERIFICAÇÃO	APROVAÇÃO
DOCUMENTOS DE REFERÊNCIA		00	EMIÇÃO INICIAL	25.07.11	ACFREIRE	TCFREIRE	GREY
			REVISÕES				



DESENHO:	TPRATA
PROJETO:	ACFREIRE
VERIFICAÇÃO:	TCFREIRE
RESP. TÉCNICO:	ACFREIRE
APROVADO:	GREY
DATA:	25.07.2011


TRANSNORDESTINA
Logística S.A.

FERROVIA TRANSNORDESTINA


TRECHO: SPS - EMT E TS		SUBTRECHO: SPS - EMT E TS	
PROJETO EXECUTIVO DE ADEQUAÇÃO PROJETO DE ADEQUAÇÃO DO SISTEMA VIÁRIO PROJETO TÍPICO PASSAGEM INFERIOR RESTRITA SIMPLES TÍPICA - ARMADURA			
ESCALA:	INDICADA	CÓDIGO:	FTN-GERAL-DE2B-1458-029
		REV:	00
		FOLHA:	1/1

ESCALA=1:25


ESCALA=1:25

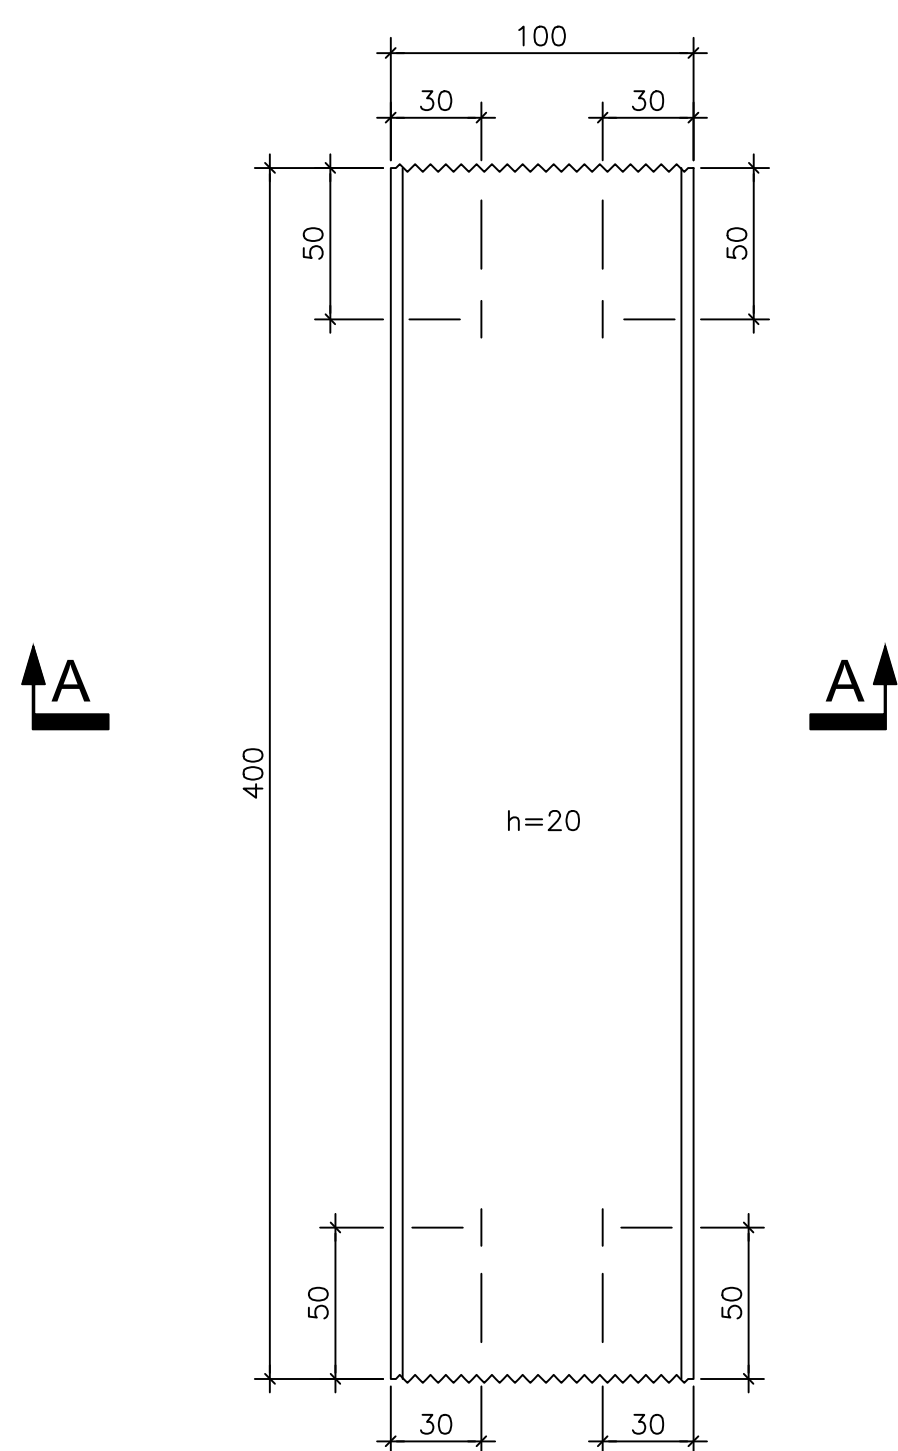


ESCALA=1:12.5

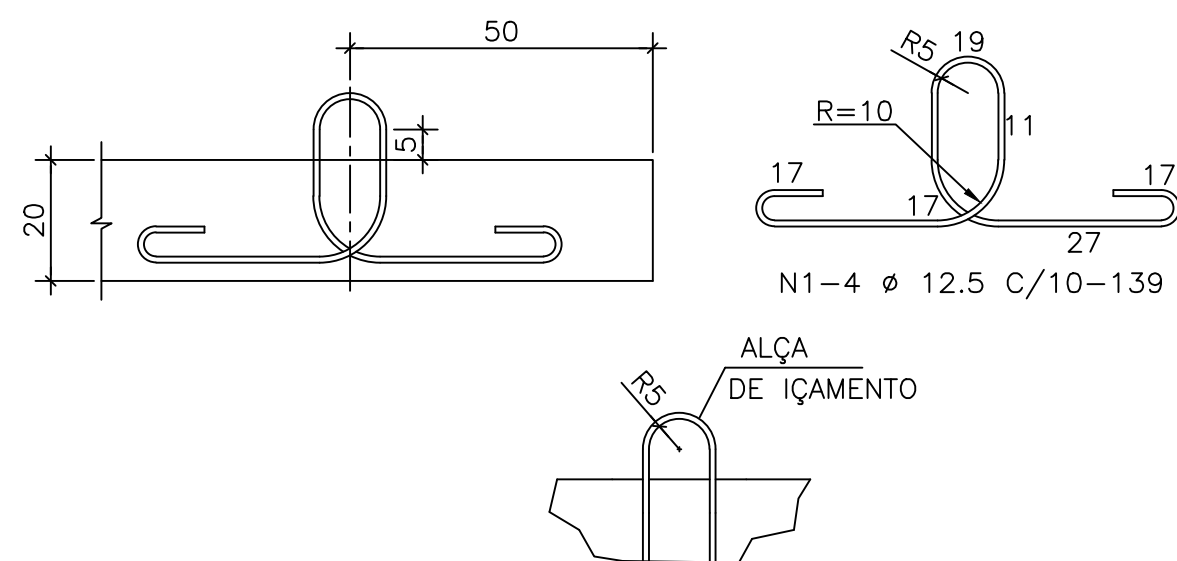


ESCALA=1:12.5

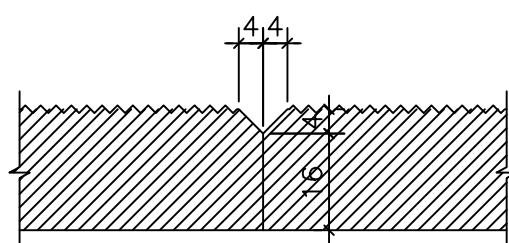


ESCALA=1:12.5

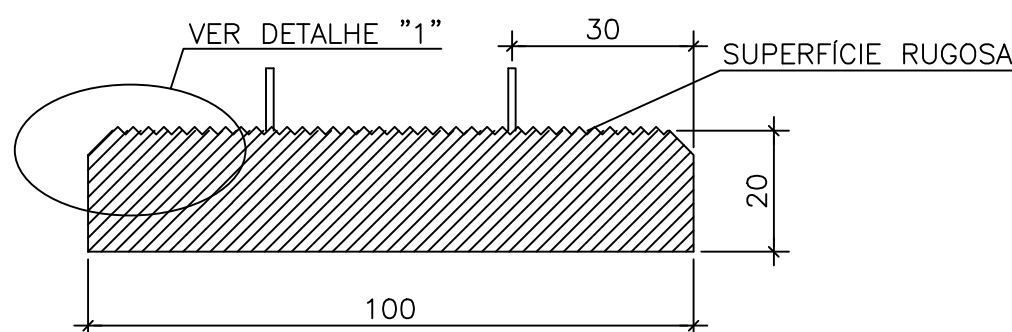


ESCALA=1:25

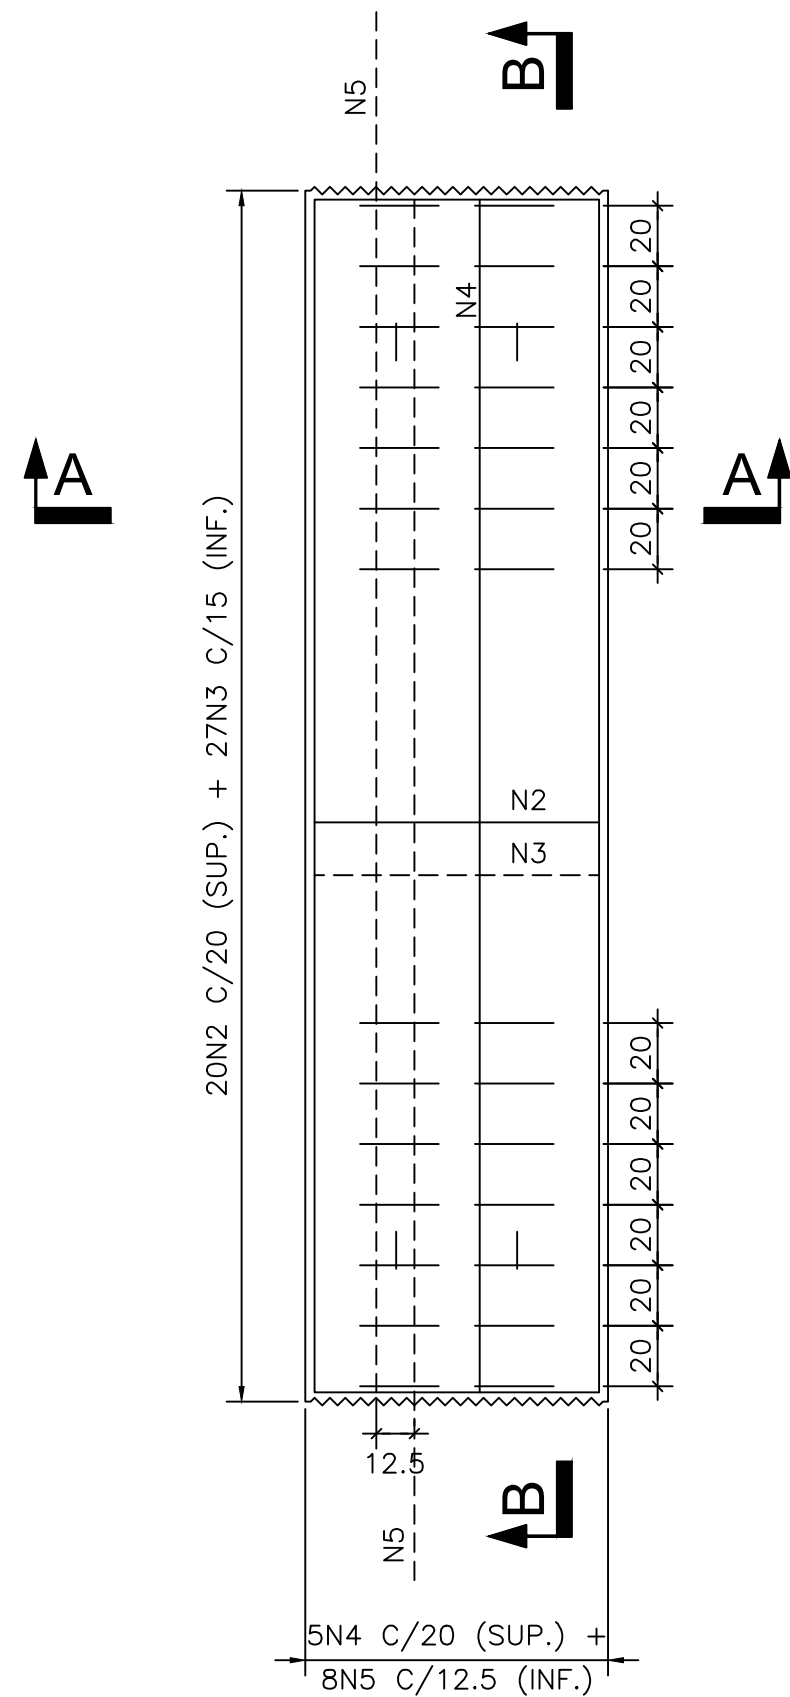

ESCALA=1:12.5

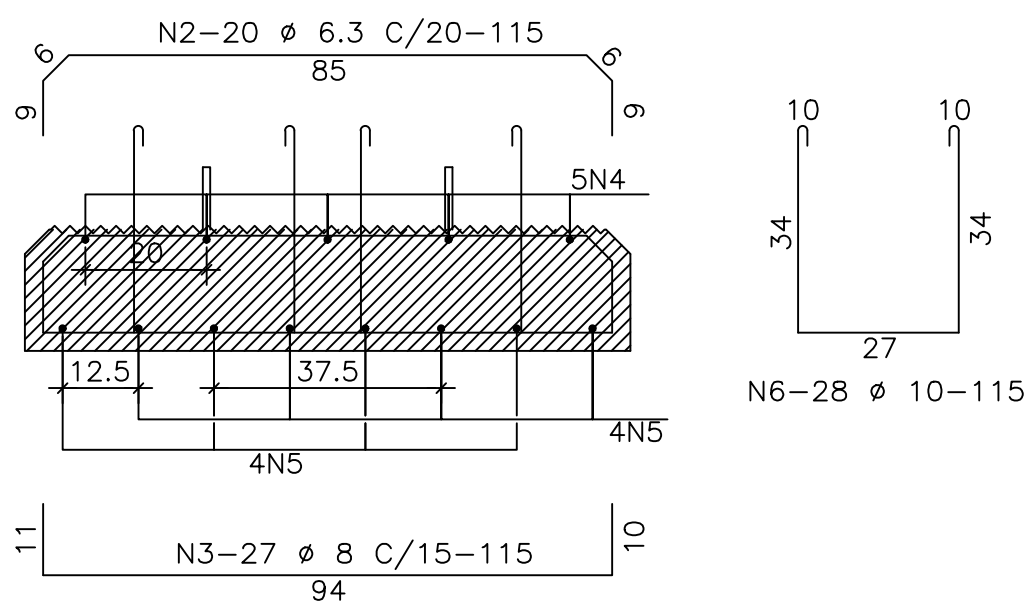

ESCALA=1:25

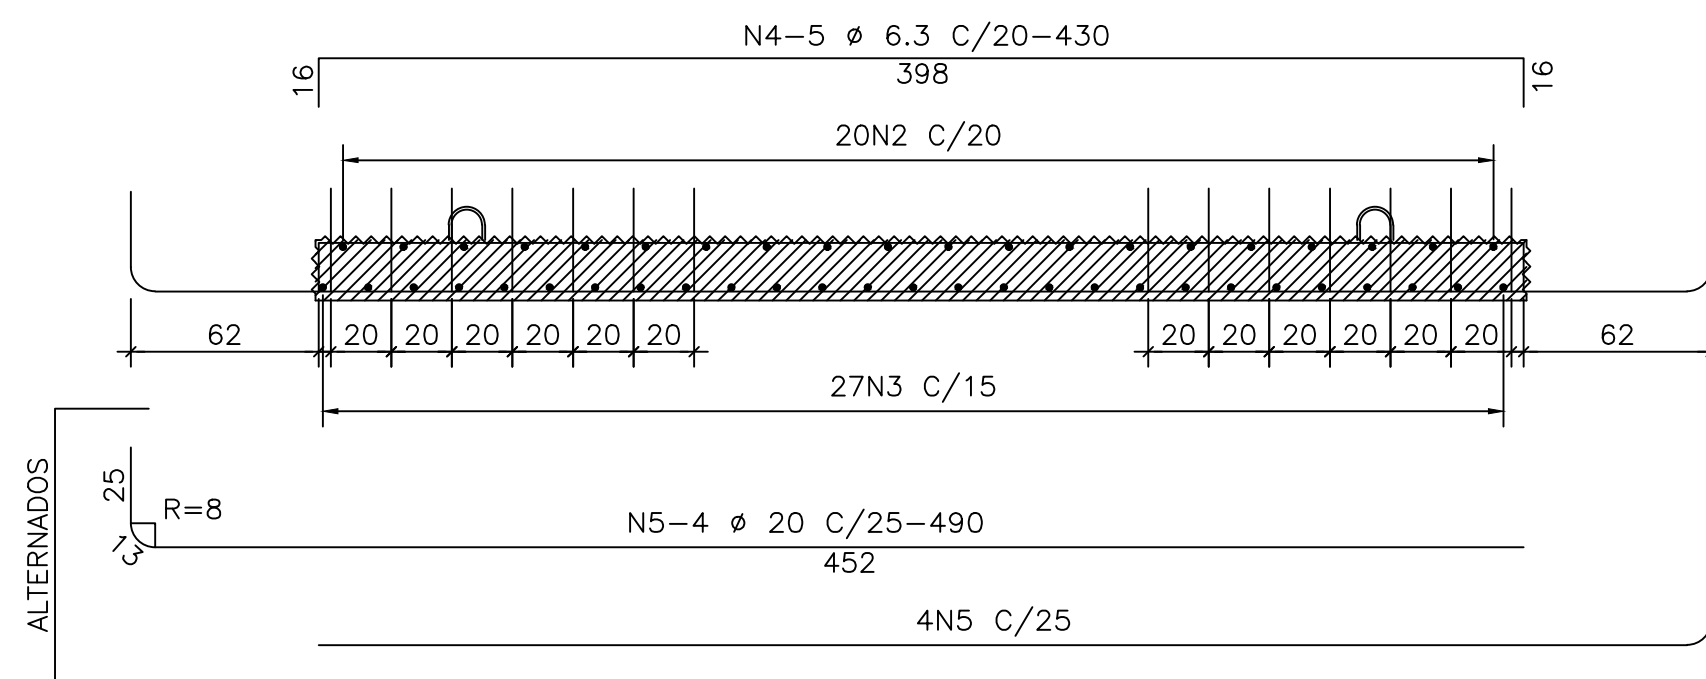


N	Ø (mm)	Q	COMPRIMENTO	
			UNIT.(cm)	TOTAL(m)
1	12.5	4	139	5.56
2	6.3	20	115	23.00
3	8	27	115	31.05
4	6.3	5	430	21.50
5	20	8	490	39.20
6	10	28	115	32.20


RESUMO CA-50		
Ø (mm)	COMPR (m)	PESO (kg)
6.3	44.50	11
8	31.05	12
10	32.20	20
20	39.20	97
TOTAL:		140

RESUMO CA-25		
Ø (mm)	COMPR (m)	PESO (kg)
12.5	5.56	5
TOTAL:		5


ESCALA=1:25

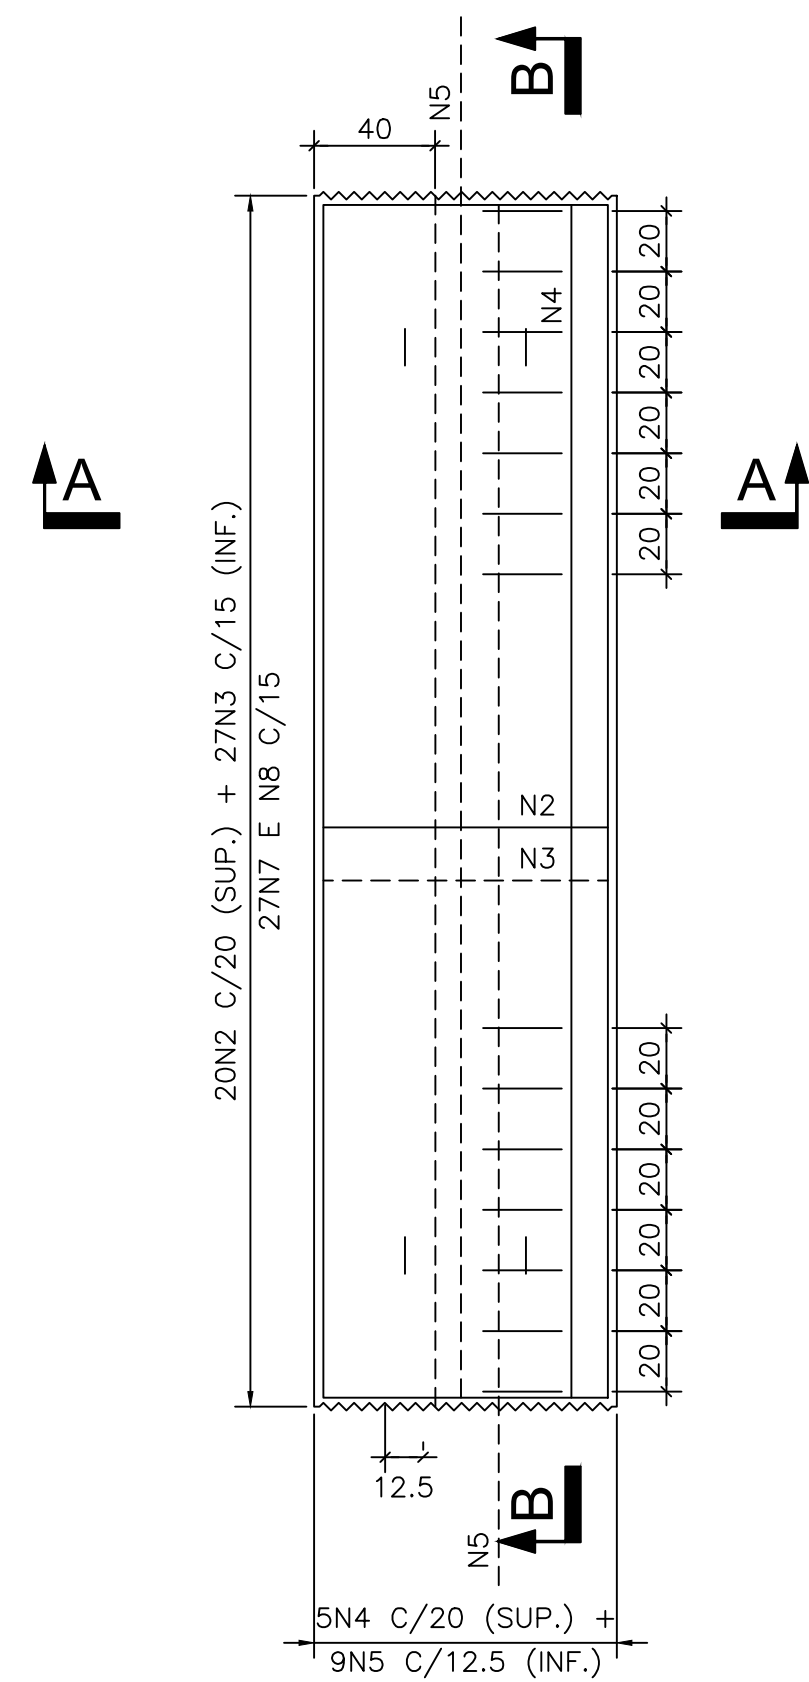

ESCALA=1:12.5

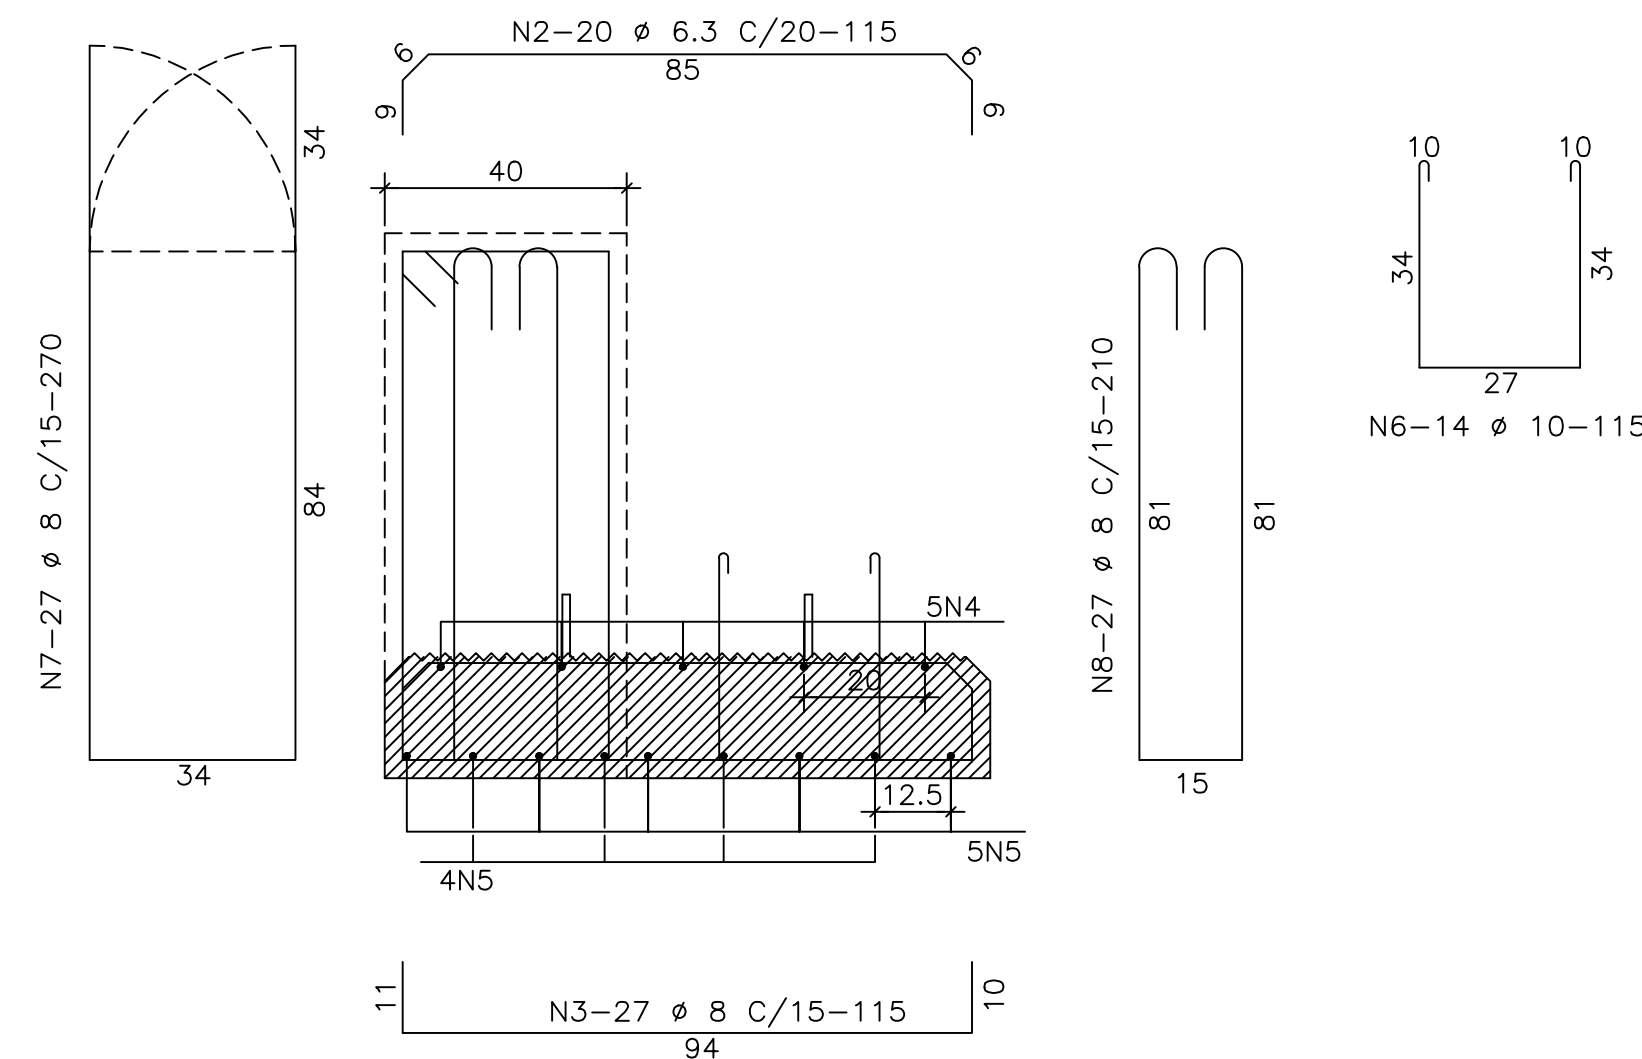

ESCALA=1:25

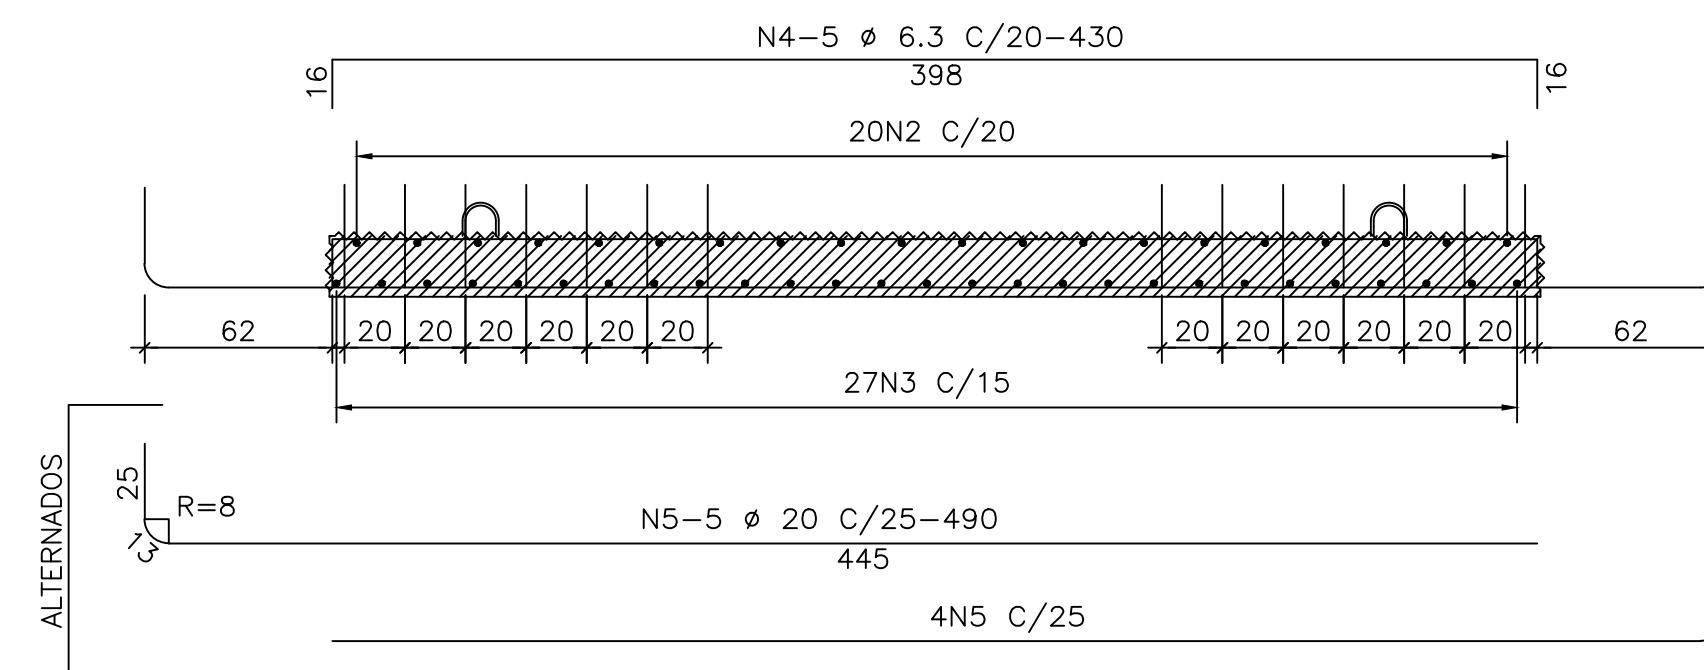

N	Ø (mm)	Q	COMPRIMENTO	
			UNIT.(cm)	TOTAL(m)
1	12.5	4	139	5.56
2	6.3	20	115	23.00
3	8	27	115	31.05
4	6.3	5	430	21.50
5	20	9	490	44.10
6	10	14	115	16.10
7	8	27	270	72.90
8	8	27	210	56.70

RESUMO CA-50		
Ø (mm)	COMPR (m)	PESO (kg)
6.3	44.50	11
8	160.65	64
10	16.10	10
20	44.10	109
TOTAL:		194

RESUMO CA-25		
Ø (mm)	COMPR (m)	PESO (kg)
12.5	5.56	5
TOTAL:		5

[illegible]

ESCALA=1:50


ESCALA=1:50



ESCALA=1:50



ESCALA=1:50

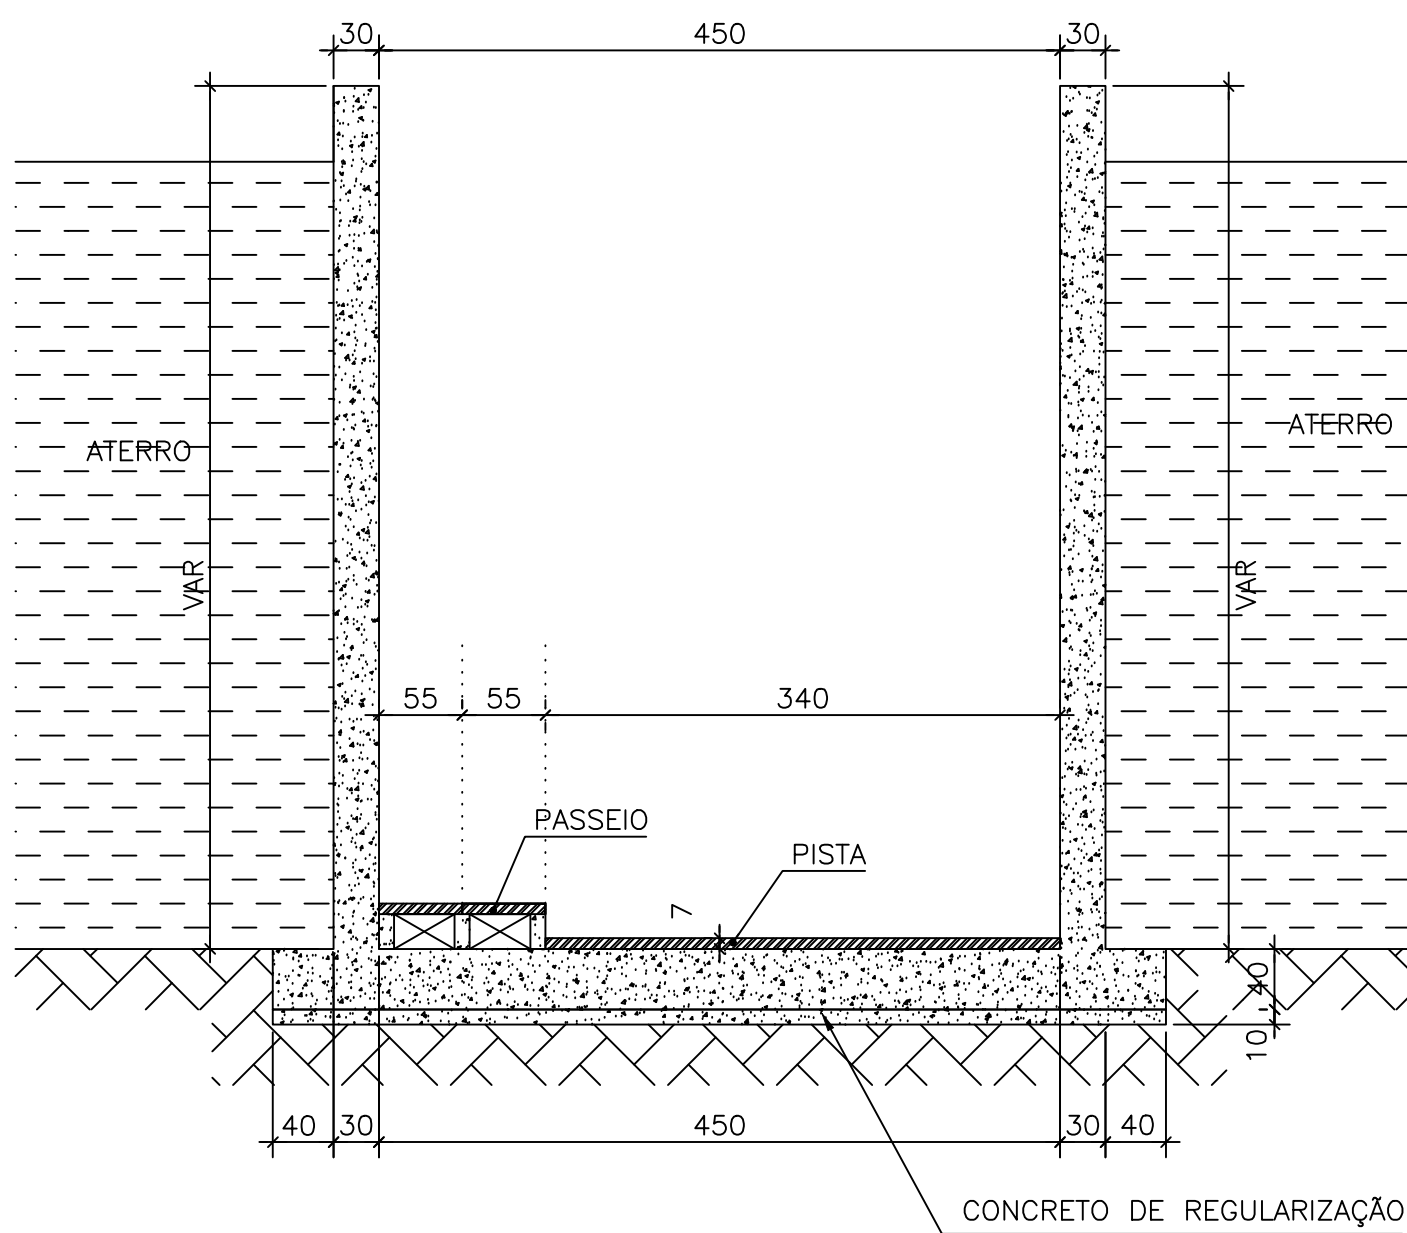

- 1_ DIMENSÕES EM CENTÍMETROS EXCETO ONDE INDICADO;
- 2_ CONCRETO ESTRUTURAL : $f_{ck} = 25 \text{ MPa}$
- 3_ OS ATERROS DEVERÃO SER COMPACTADOS SIMULTANEAMENTE NOS DOIS LADOS E COMPACTADOS COM ESPESURA NÃO SUPERIOR A 25 cm.
- 4_ DEPENDENDO DO COMPORTAMENTO DO ATERRO, PODERÃO SER INCORPORADAS LAJES DE APROXIMAÇÃO ÀS OBRAS.
- 5_ TRECHO EM PIR, A TENSÃO NO TERRENO É ALIVIADA EM COMPARAÇÃO AO MESMO TRECHO SOLO ATERRO.


[illegible]



ESCALA=1:50





ESCALA=1:50

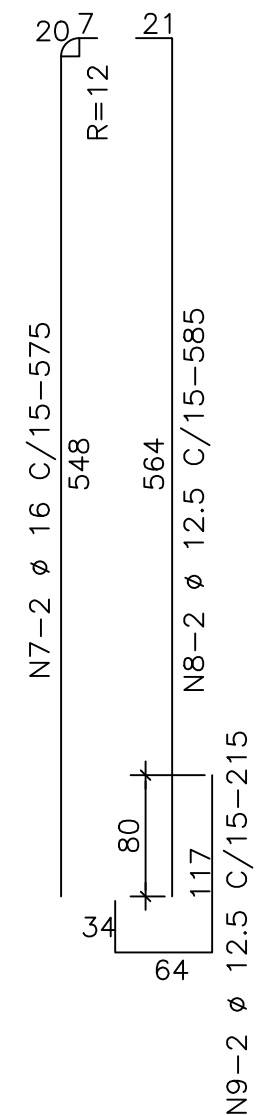

ESCALA=1:50



TOTAL PARA 3 PIR'S	
TOTAL(x3):	21.918

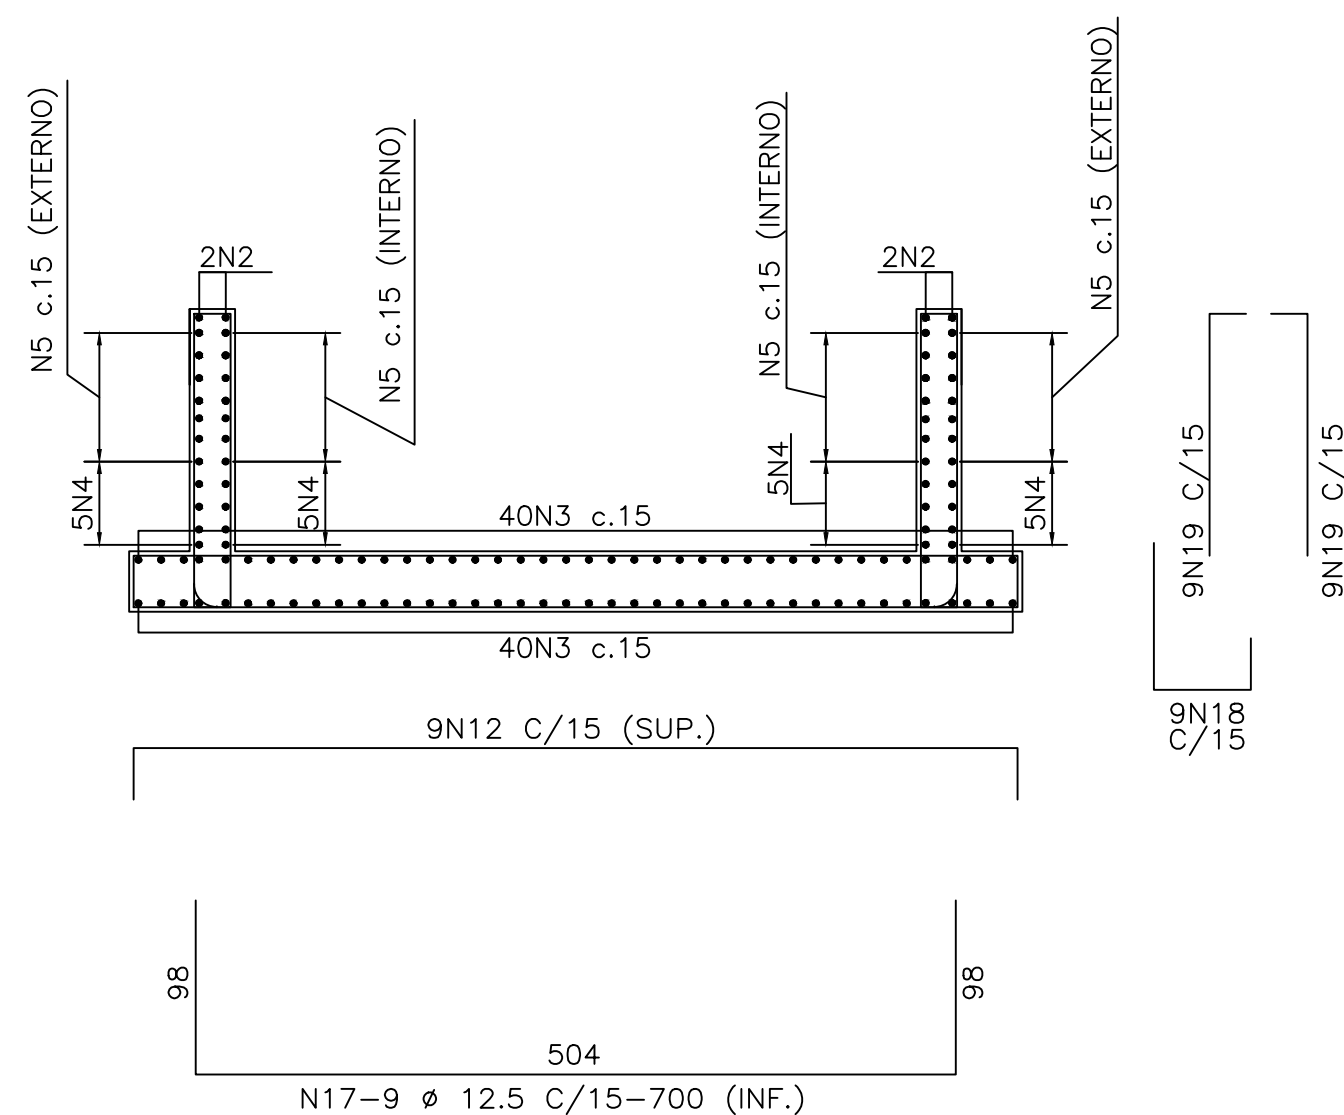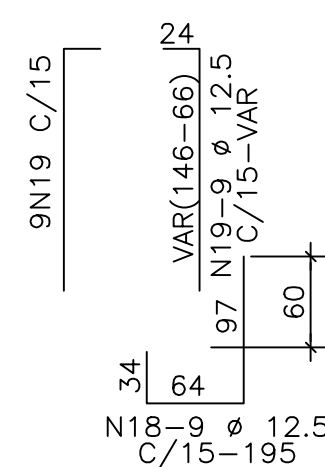

1_ DIMENSÕES EM CENTÍMETROS EXCETO ONDE INDICADO;
2_ CONCRETO ESTRUTURAL : $f_{ck} = 25 \text{ MPa}$
3_ OS ATERROS DEVERÃO SER COMPACTADOS SIMULTANEAMENTE NOS DOIS LADOS
E COMPACTADOS COM ESPESURA NÃO SUPERIOR A 25 cm.
4_ COBRIMENTO = 3cm

Nº	OBJETO	REV.	DESCRIÇÃO	DATA	ELABORAÇÃO	VERIFICAÇÃO	APROVAÇÃO
	DOCUMENTOS DE REFERÊNCIA	00	EMISSION INICIAL	17.08.11	ACFREIRE	TCFREIRE	GREY
			REVISÕES				

**BETON
STAHL**
Engenharia Ltda

TRANSNORDESTINA

FERROVIA TRANSNORDESTINA

TRECHO: SPS - EMT E TS

PROJETO EXECUTIVO DE ADEQUAÇÃO

PROJETO DE AD


PROJETO TÍPICO
PASSAGEM INFERIOR RESTRITA TÍPICA - ARMADURA DAS

ESCALA: INDICADA


CÓDIGO: ETALCE04.0520.4459.04

REV.:	FOLHA:
-------	--------


ESCALA=1:25

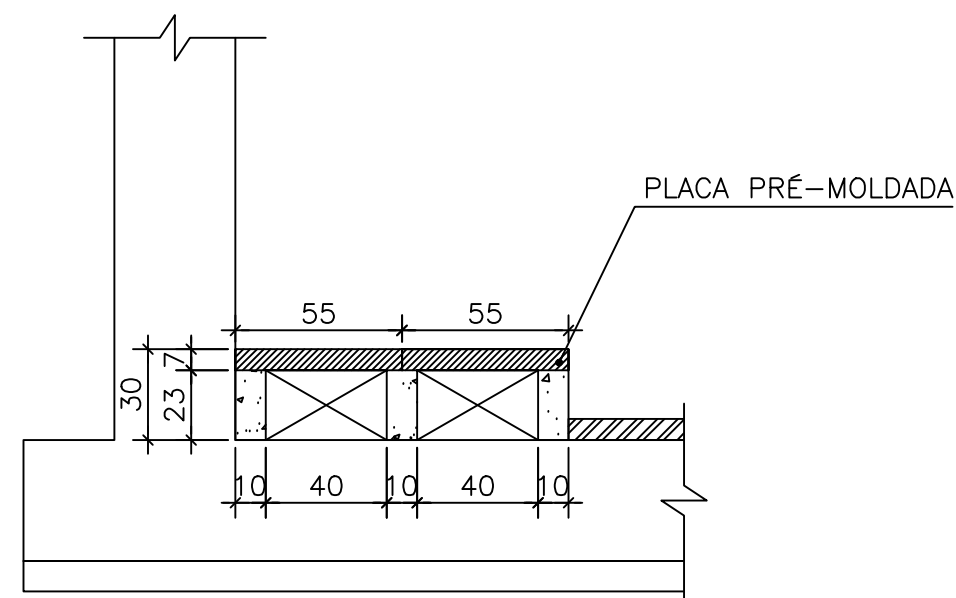


ESCALA=1:25

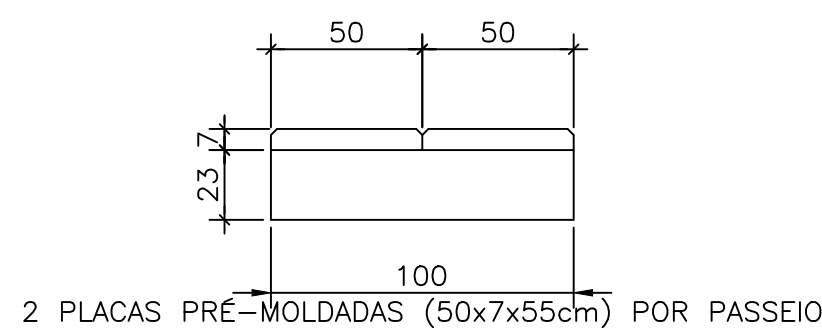


ESCALA=1:25

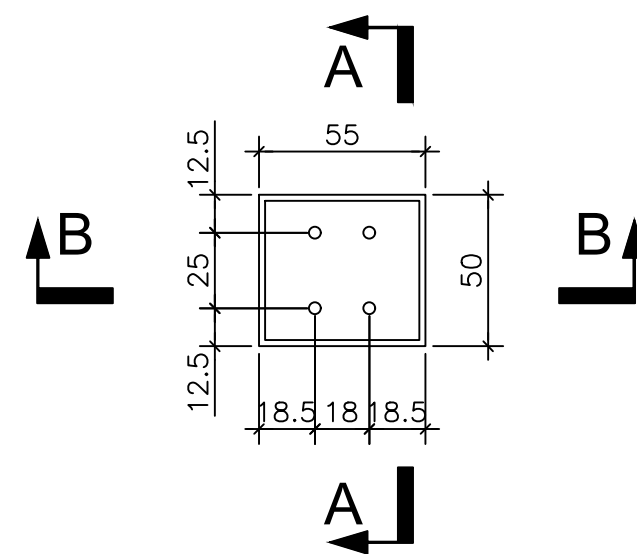


ESCALA=1:12.5

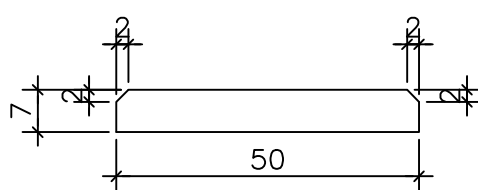


ESCALA=1:12.5

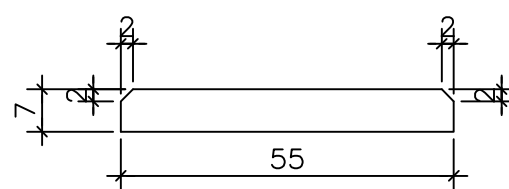

ESCALA=1:12.5

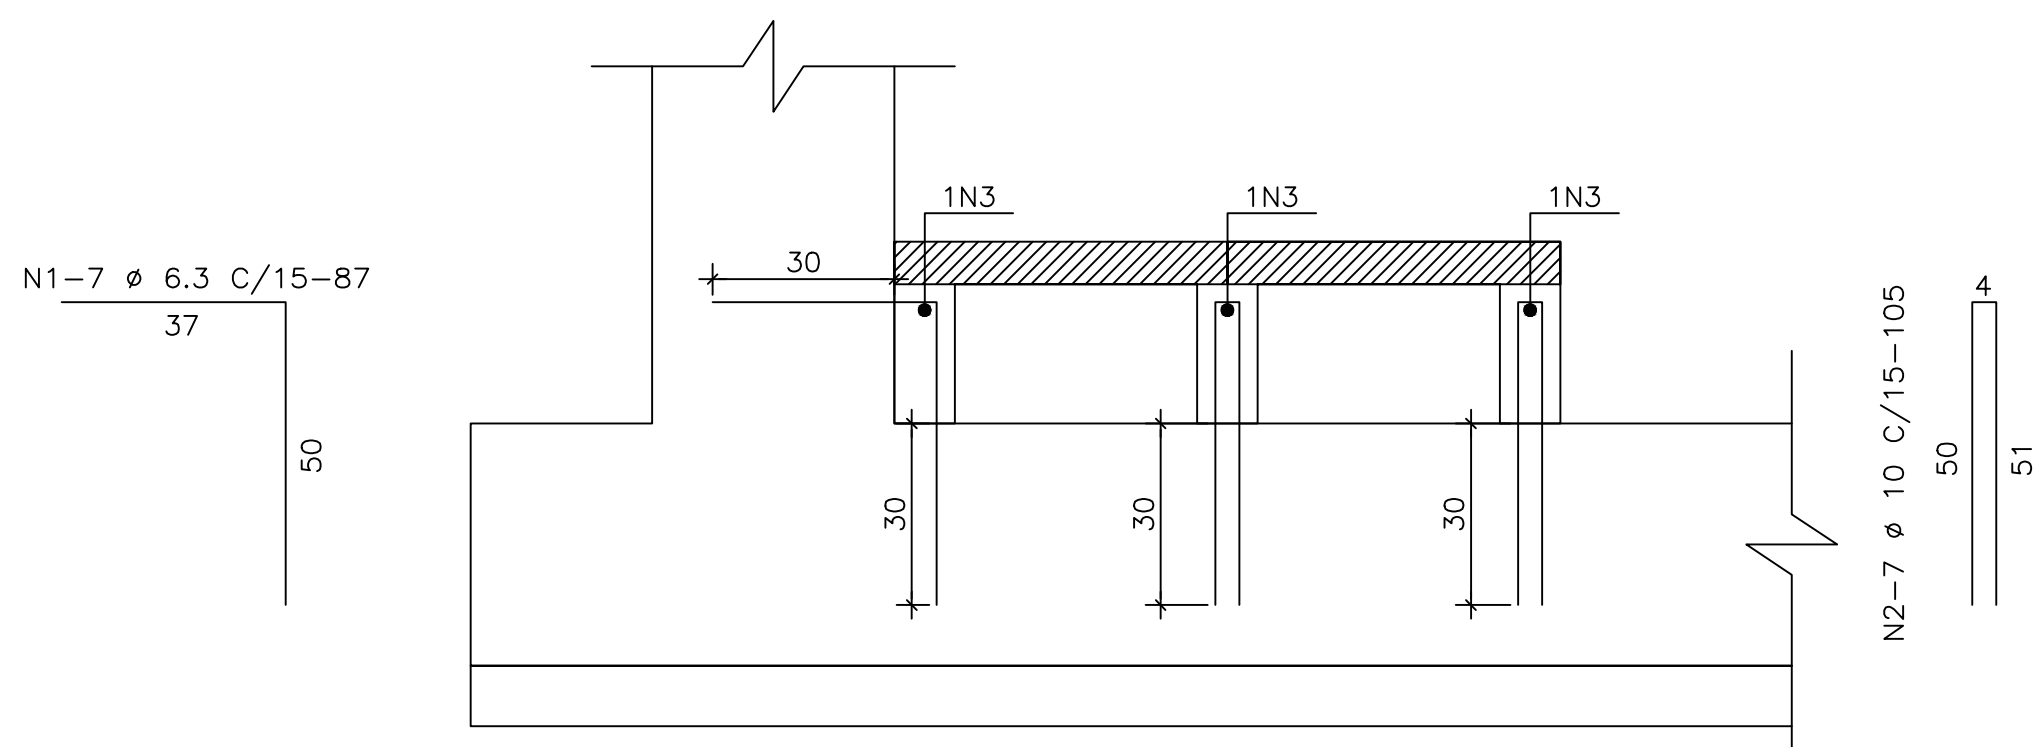


ESCALA=1:12.5

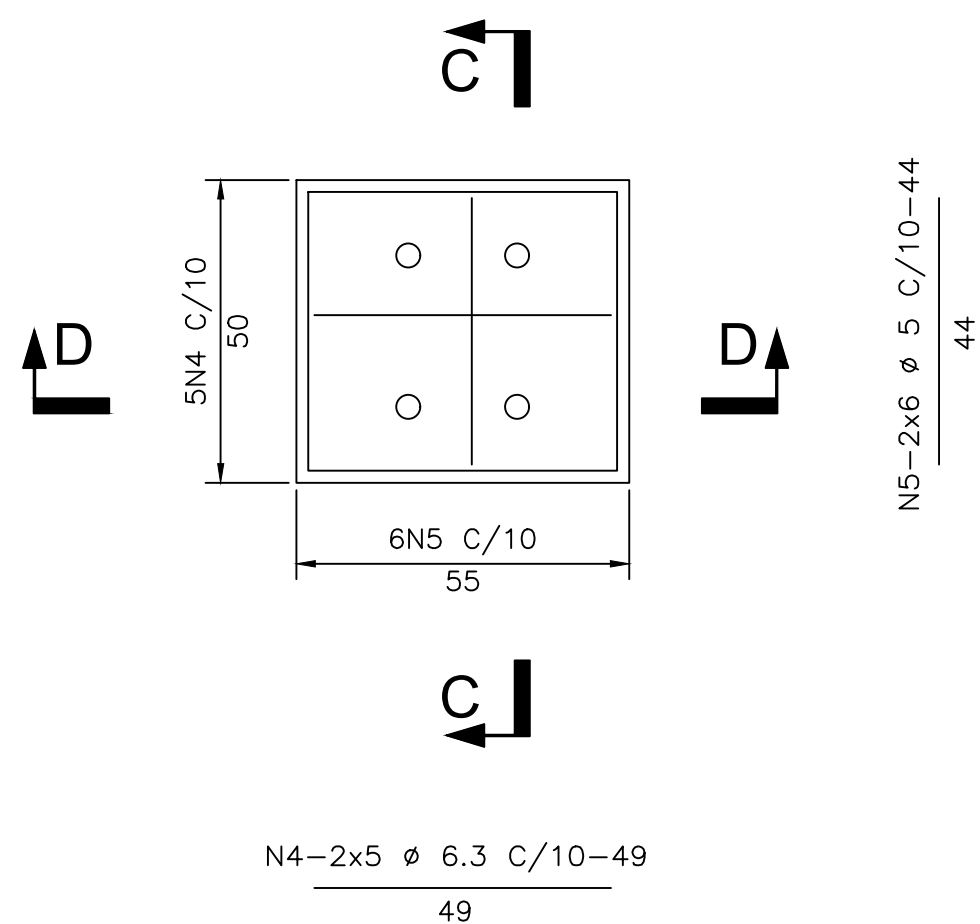

N	Ø (mm)	Q	COMPRIMENTO	
			UNIT.(cm)	TOTAL(m)
1	6.3	7	87	6.09
2	10	7	105	7.35
3	10	3	CORRIDO	3.84
4	6.3	20		49
5	5	24	44	10.56


RESUMO CA-50		
Ø (mm)	COMPR (m)	PESO (kg)
5	10.56	2
6.3	15.89	4
10	11.19	7
TOTAL:		13

ESCALA=1:50

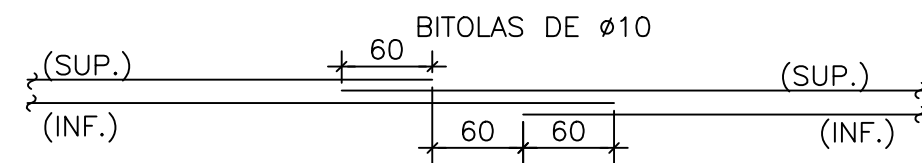


ESCALA=1:25


N3-3x1 Ø 10-CORR (COM EMENDAS DEFASADAS DE 60 cm)

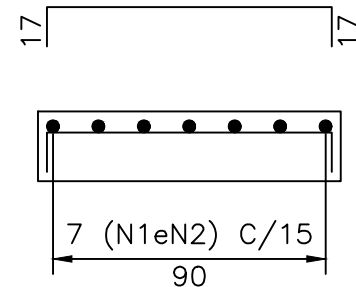

S/ESCALA

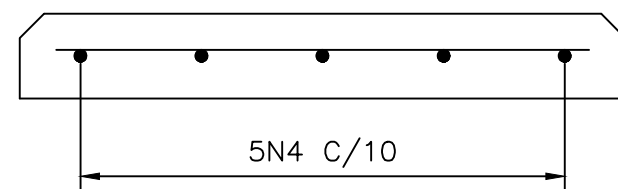

S/ESCALA

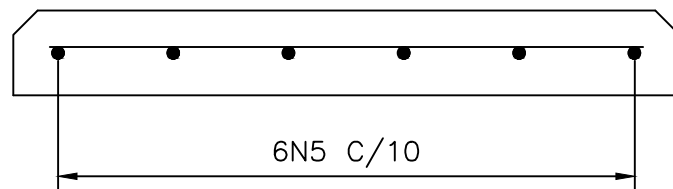

1_ DIMENSÕES EM CENTÍMETROS EXCETO ONDE INDICADO;
2_ CONCRETO ESTRUTURAL : fck= 25 MPa
3_ OS ATERROS DEVERÃO SER COMPACTADOS SIMULTANEAMENTE NOS DOIS LADOS E COMPACTADOS COM ESPESSURA NÃO SUPERIOR A 25 cm.
4_ COBRIMENTO = 3cm
5_ ESTE DESENHO PODE SER UTILIZADO PARA TODAS AS INCLINAÇÕES.

N°	OBJETO	REV.	DESCRIÇÃO	DATA	ELABORAÇÃO	VERIFICAÇÃO	APROVAÇÃO
		00	EMISSION INICIAL	06.09.11	ACFREIRE	TCFREIRE	GREY
	DOCUMENTOS DE REFERÊNCIA		REVISÕES				

 BETON STAHL Engenharia Ltda	TRANSNORDESTINA <i>Logística S.A.</i>			
	FERROVIA TRANSNORDESTINA			
DESENHO: TP/ATA	TRECHO-SPS - EMT E TS	SUBTRECHO: SPS - EMT E TS		
PROJETO: AC/FRÉIRE	PROJETO EXECUTIVO DE ADEQUAÇÃO			
VERIFICAÇÃO: TCF/REIRE	PROJETO DE ADEQUAÇÃO DO SISTEMA VIÁRIO			
APR. TÉCNICO: AC/FRÉIRE	PROJETO TÍPICO			
APPROVAÇÃO: GREY	PASSAGEM INFERIOR RESTRITA SIMPLES TIPO - FORMA E ARMADURA DOS PASSAGIOS			
DATA: 06.09.2011	ESCALA: 1:1	CODIGO: FTM-GERAL-DE2B-1458-055	REV: 00	FOLHA 1/1