


SEÇÃO TIPO DE EMPRÉSTIMO

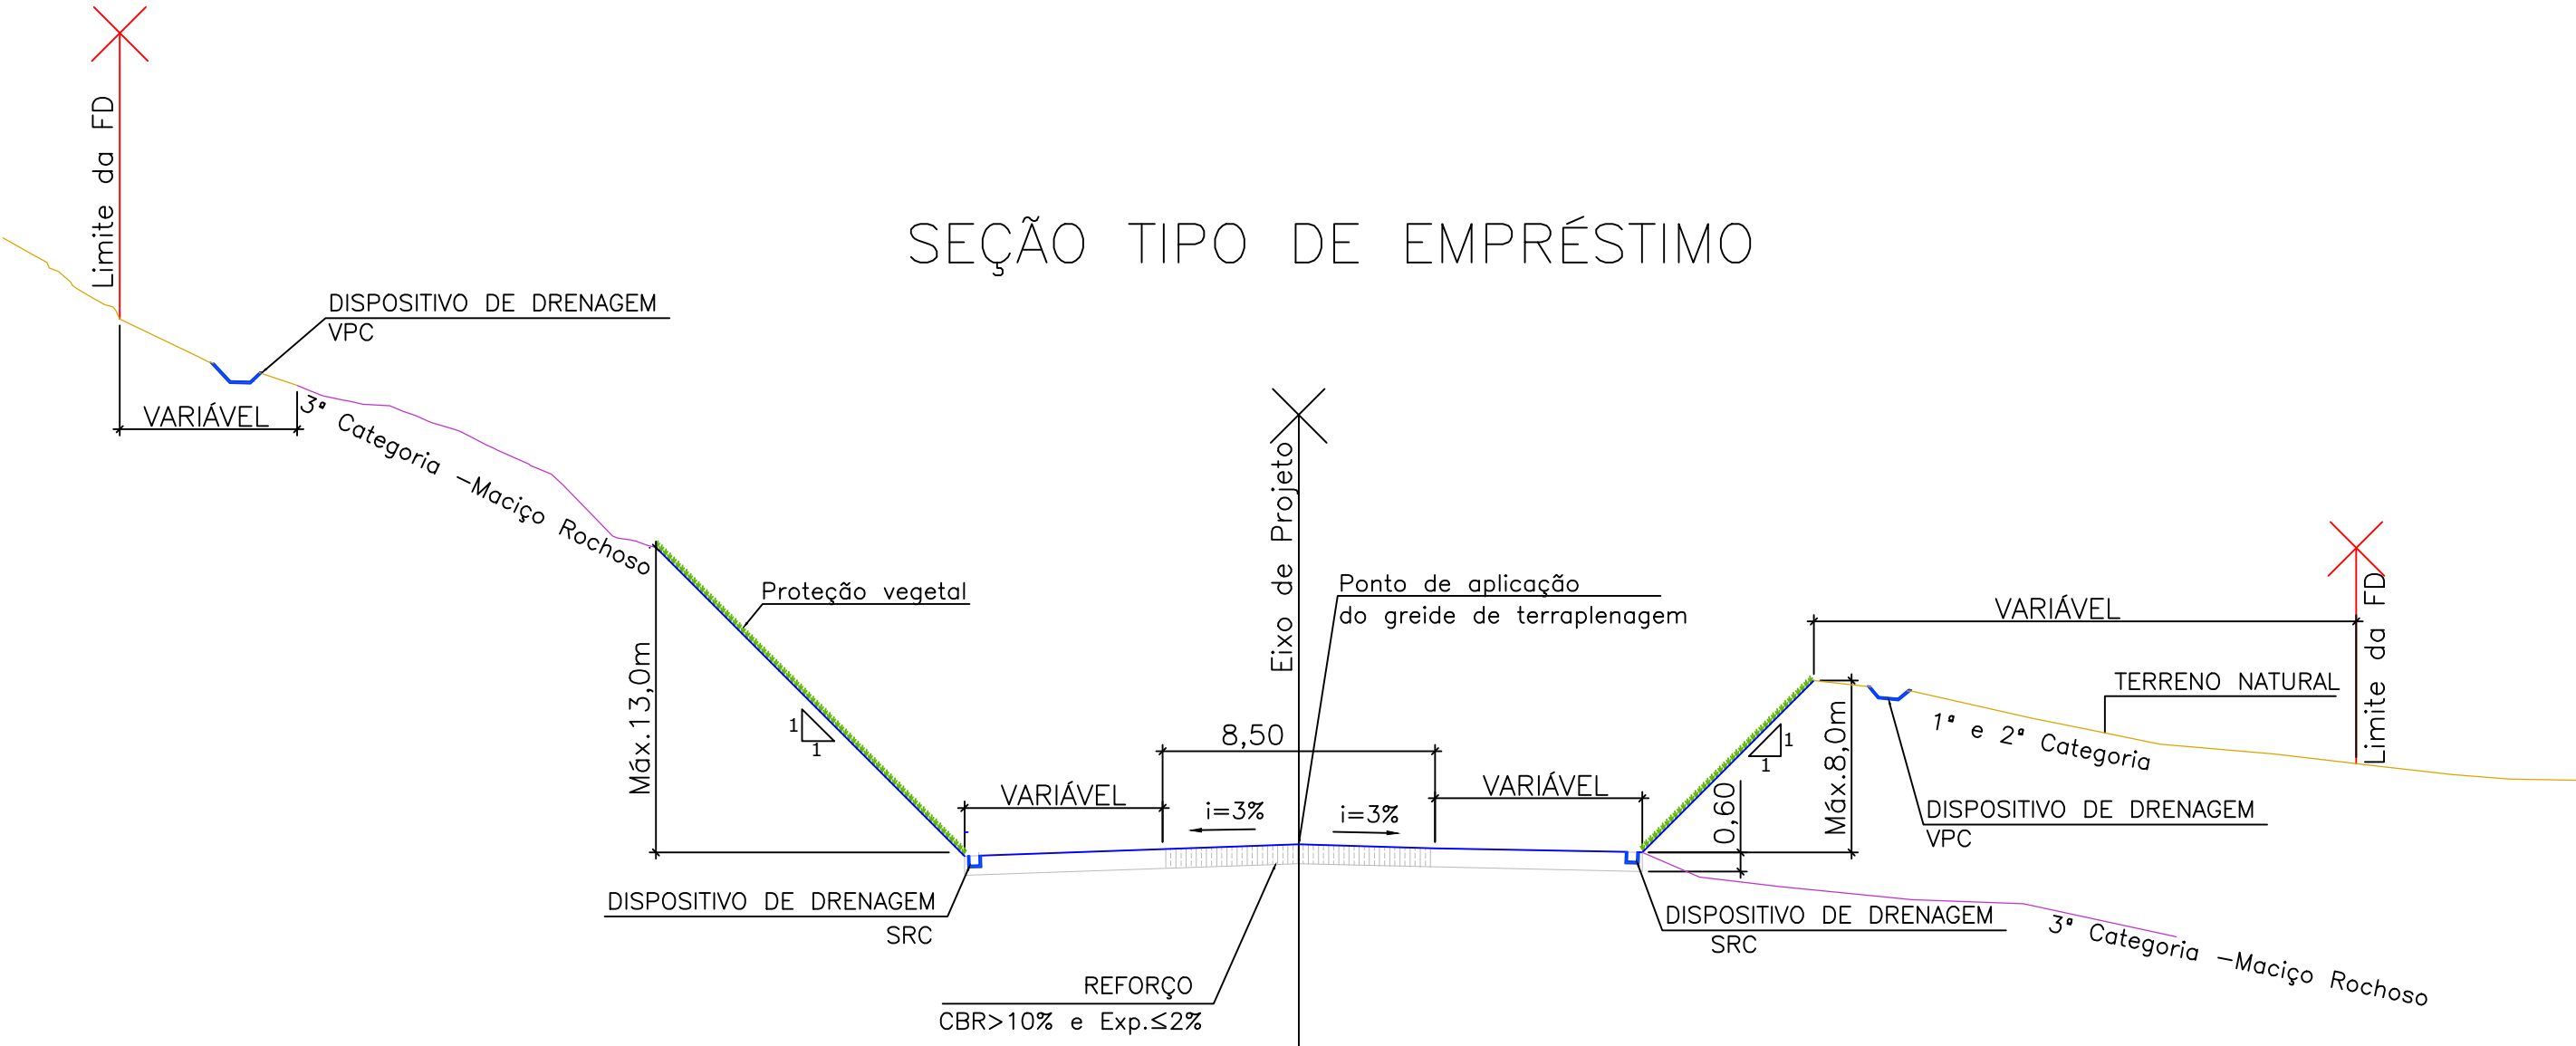

TODAS AS MEDIDAS ESTÃO EM METRO, EXCETO ONDE INDICADO

NOTA 1: DISPOSITIVOS DE DRENAGEM (VER PROJETO ESPECÍFICO)

VPC = VALETA DE PROTEÇÃO DE CORTE

VPBC = VALETA DE PROTEÇÃO DE BANQUETA DE CORTE

SRC = SARJETA RETANGULAR DE CORTE

NOTA 2: O PREENCHIMENTO DO REATERRO E/OU SUBSTITUIÇÃO E/OU REFORÇO NÃO DEVE SE ESTENDER ALÉM DA LARGURA DA PLATAFORMA, SENDO 8,50 m PARA TRECHOS DE LINHA SIMPLES E 13,50 m PARA TRECHOS DE PÁTIO DE CRUZAMENTO

NOTA 3: NOS CORTES EM SOLO ADOTOU-SE BANQUETAS A CADA 8,00 m COM TOLERÂNCIA DE 1,00 m PARA A ÚLTIMA BANQUETA.

NOTA 4: DURANTE A OBRA, ATENTAR PARA O DESMONTE DOS MACIÇOS, POIS CASO SEJAM ENCONTRADAS ROCHAS LAMINADAS, FACILMENTE FRAGMENTÁVEIS, COMO POR EXEMPLO, XISTOS E FILITOS, ESTAS NÃO DEVERÃO SER ADMITIDAS NO CORPO DE ATERRO OU EM CAMADA FINAL. CONSEQUENTEMENTE ESTE MATERIAL DEVERÁ SER DESTINADO AOS DEPÓSITOS DE MATERIAL EXCEDENTE.

SEG.	INÍCIO	FINAL	INCLINAÇÃO TALUDES	ALTURA MÁX. BERMAS	EMPRÉSTIMO	
					LE(m)	FD(m)
1	434+320	434+365	1(V):1(H)	—	3	30
2	434+365	434+480	1(V):1(H)	—	6	30

						LEGENDA: CAMADA VEGETAL TERRENO NATURAL SUPERFÍCIE PROJETO BASE - CAMADA FINAL (ATERRO) TOPO - TRANSIÇÃO (ATERRO) TOPO - ATERRO ROCHOSO (ATERRO) HACHURA - REBAIXO/SUBST. 1ª/2ª CAT. HACHURA - REBAIXO/SUBST. 3ª CAT. SUPERFÍCIE 2ª CAT (CORTE). SUPERFÍCIE 3ª CAT. (CORTE) SUPERFÍCIE EXEC. - LEV. OBRA HACHURA - CORTE/EMPR. 1ª CAT. HACHURA - CORTE/EMPR. 2ª CAT. HACHURA - CORTE/EMPR. 3ª CAT. HACHURA - BOTAFORA HACHURA - CAMADA FINAL HACHURA - ATERRO SOLO HACHURA - TRANSIÇÃO HACHURA - ATERRO ROCHA						TLSA TRANSPORTES LOGÍSTICA S.A.		TRANSPORTES LOGÍSTICA S.A.					
						LINHA: FERROVIA TRANSPORTES LOGÍSTICA S.A. TRECHO: MISSÃO VELHA - PORTO DO PECÉM													
						SUB-TRECHO: MVP-09 OBJETO: PROJETO EXECUTIVO - PROJETO DE TERRAPLENAGEM FOLHA: 012													
						ESCALA: H - 1:1000 V - 1:2000		SEÇÃO TIPO EMPRESTIMO KM 434+320 A 434+480		DESENHO Nº FTN-MVP09-TI4D-0643-001		REV. 00							
00 EMIÇÃO INICIAL 26/05/2026 RKRD LAPB UAS																			
Nº DESCRIÇÃO DATA EMITENTE VERIFICAÇÃO APROVAÇÃO																			
REVISÕES																			